


SHEET INDEX


- 1 C1 TITLE PAGE & PROPOSED SITE PLAN
2 C2 EXISTING SITE PLAN/TOPOGRAPHIC SURVEY
3 C3 BMP PLAN, CALCS. & DETAILS
4 C4 DEFENSIBLE SPACE PLAN
5 A1 PROPOSED FLOOR PLANS
6 A2 ROOF PLAN, SCHEDULES & ELECTRICAL NOTES
7 A3 PROPOSED HOUSE ELEVATIONS
8 A4 PROPOSED HOUSE ELEVATIONS
9 A5 EXTERIOR ISOMETRIC VIEWS
10 A6 INTERIOR ISOMETRIC VIEWS
11 A7 BUILDING SECTION & ARCHITECTURAL DETAILS
12 E1 ELECTRICAL & GAS PIPING PLANS
13 E2 TITLE 24 ENERGY CALCULATIONS
14 G1 ARCHITECTURAL NOTES
15 G2 WILDLAND-URBAN INTERFACE CODES
16 G3 CALGREEN MANDATORY MEASURES PART 1
17 G4 CALGREEN MANDATORY MEASURES PART 2
18 S1.1 STRUCTURAL GENERAL NOTES
19 S2.1 FOUNDATION DIMENSION PLAN
20 S2.2 FOUNDATION & LOWER FLOOR FRAMING PLAN
21 S2.3 UPPER FLOOR FRAMING PLAN
22 S2.4 UPPER FLOOR LATERAL SYSTEM PLAN
23 S2.5 ROOF FRAMING PLAN
24 S2.6 ROOF LATERAL SYSTEM PLAN
25 S3.1 FOUNDATION DETAILS
26 S3.2 FLOOR & ROOF FRAMING DETAILS
27 S3.3 ROOF DETAILS

795 COLUMBINE CIRCLE Lot 518

NEW SINGLE FAMILY DWELLING 2025

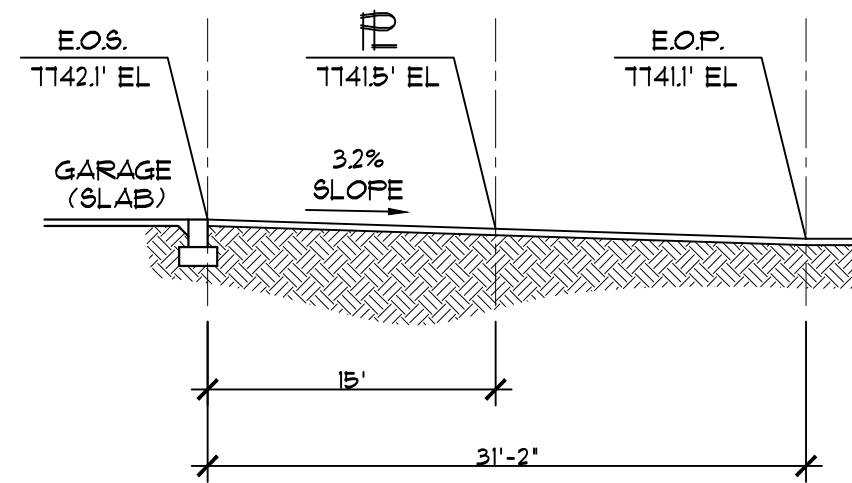

DRIVEWAY PROFILE
SCALE: 1"=10'

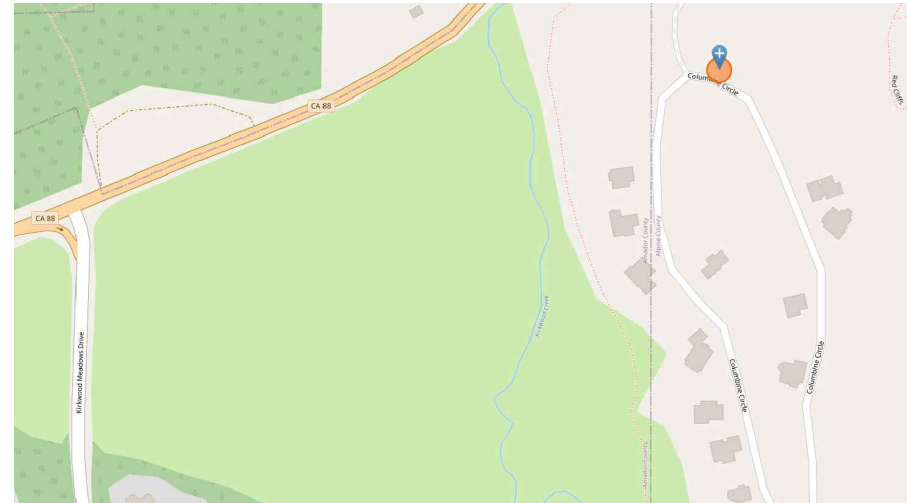

OWNER:
JUSTIN GRIFFIN
1550 DINA COURT
SAN JOSE, CA 95121
P: 617.513.3844
E: CAPPYJTG@GMAIL.COM

LEGAL DESCRIPTION:
Lot 518, East Meadows Sub. Unit No. 2
Alpine County, California 95646

Street Address: 795 Columbine Circle

APN: 006-152-001

Lot Area: 49,166 sf (1.128 Acres)

SCOPE OF WORK

NEW CONSTRUCTION SINGLE FAMILY
RESIDENCE, 2,882 SF 4 BEDROOMS,
3 BATHROOMS & 887 SF 2 CAR
GARAGE/WORKSHOP

PROPOSED LIVING SPACE

FLOOR AREA:	PROPOSED
UPPER FLOOR	1,849 S.F.
LOWER FLOOR	1,033 S.F.
FLOOR AREA TOTAL	2,882 S.F.
GARAGE AREA	887 S.F.

BUILDING CODE DATA
OCCUPANCY GROUP = R-3, U-1
TYPE OF CONSTRUCTION = V-B
STORIES = 2
ZONING = PLANNED DEVELOPMENT FOR KIRKWOOD EAST MEADOWS
FIRE SPRINKLERS = YES
TOTAL PROPOSED CONDITIONED AREA = 2,882 SF

TOTAL PARCEL AREA:	49,166 SF
ALLOWABLE BUILDING FOOTPRINT AREA:	8,225 SF
MAXIMUM ALLOWABLE COVERAGE:	3,500 SF

PROPOSED COVERAGE TABLE:

TYPE:	AREA:	COVERAGE INSIDE ENVELOPE:
RESIDENCE/GARAGE	1,922 SF	1,922 SF
REAR DECKS & STAIRS	464 SF	464 SF
FRONT DECK & STAIRS	198 SF	156 SF
OVERHANGS	12 SF	10 SF
WOOD FRAMED DRIVEWAY	301 SF	124 SF
TOTAL LAND COVERAGE:	2,897 SF	2,676 SF
BANKED COVERAGE:		824 SF

DRAFTING/DESIGN FIRM:

JA DESIGNS
SHELDON BIDWELL
PO BOX 9437
SOUTH LAKE TAHOE, CA 96158
PHONE: 530-600-2779
EMAIL: DONEBIDSLT@YAHOO.COM

SPECIAL INSPECTIONS REQUIRED:

- SB407 APPLIES (REQUIRED BEFORE FINAL INSPECTION)
- HERS TEST (REQUIRED BEFORE FINAL INSPECTION)

DEFERRED SUBMITTALS:

- NONE

1) CONSTRUCTION NOTES

CONTRACTOR TO VERIFY ALL
DIMENSIONS AND SITE CONDITIONS
SHOWN AND TO NOTIFY JA DESIGNS
OF ANY DISCREPANCIES PRIOR
TO COMMENCEMENT OF WORK.

2) CODES

THIS PROJECT SHALL COMPLY WITH
ALL APPLICABLE BUILDING CODES AS
SHOWN BELOW & CODES THAT WERE IN EFFECT
AT THE TIME OF NON-PERMITTED CONSTRUCTION:
● 2025 CALIFORNIA BUILDING CODE (CBC)
(INCLUDING ASCE 1-05 (FOR STRUCTURAL))
● 2025 CALIFORNIA RESIDENTIAL CODE (CRC)
(FOR NON-STRUCTURAL)
● 2025 WILDLAND URBAN INTERFACE CODE (WUI)
PER CRC R33.1
● 2025 CALIFORNIA PLUMBING CODE (CPC)
● 2025 CALIFORNIA MECHANICAL CODE (CMC)
● 2025 CALIFORNIA ELECTRICAL CODE (CEC)
● 2025 CALIFORNIA FIRE CODE
● 2025 CALIFORNIA ENERGY CODE
● 2025 CALIFORNIA GREEN BUILDING
STANDARDS CODE - WHERE APPLICABLE
AND ANY OTHER PERTINENT LOCAL
CODES & ORDINANCES

3) NOTES

- NOTE: DRIVEWAY TO BE MIN. 2'-1/2" A/C OVER
4" A/C OR SEALED CONC. OR 4" COMPACTED AGG. BASE
- MOTION LIGHT ABOVE GARAGE DOOR FOR SNOW REMOVAL
- EXTERIOR LIGHTING TO BE DARK SKY APPROVED
- INSTALL PROPANE DETECTORS PER ELECTRICAL PLANS
- TEMPORARY POWER SHALL NOT BE NAILED TO TREES
- SURPLUS SOIL TO BE REMOVED FROM SITE & DISPOSED OF
INSTALL IRRIGATION FOR RE-VEGETATION

TOPOGRAPHIC SOURCE:

A FIELD SURVEY WAS PERFORMED BY WDH LAND
SURVEYING ON JUNE 09, 2023.

CONTOUR INTERVAL = 1'


ASSUMED ELEVATION - 6227.82'

TEMPORARY BENCHMARK #1 IS A NAIL IN A.C. PAVING
ASSUMED ELEVATION IS (7740.33')

TEMPORARY BENCHMARK #2 IS A NAIL IN A.C. PAVING
ASSUMED ELEVATION IS (7735.51')

TEMPORARY BENCHMARK #3 IS A NAIL IN A.C. PAVING
ASSUMED ELEVATION IS (7722.36')

NOTE:
THIS DOCUMENT IS NOT INTENDED TO REPRESENT A
BOUNDARY SURVEY. PROPERTY BEARINGS AND
DISTANCES SHOWN ARE RECORD DATA PER (R1).

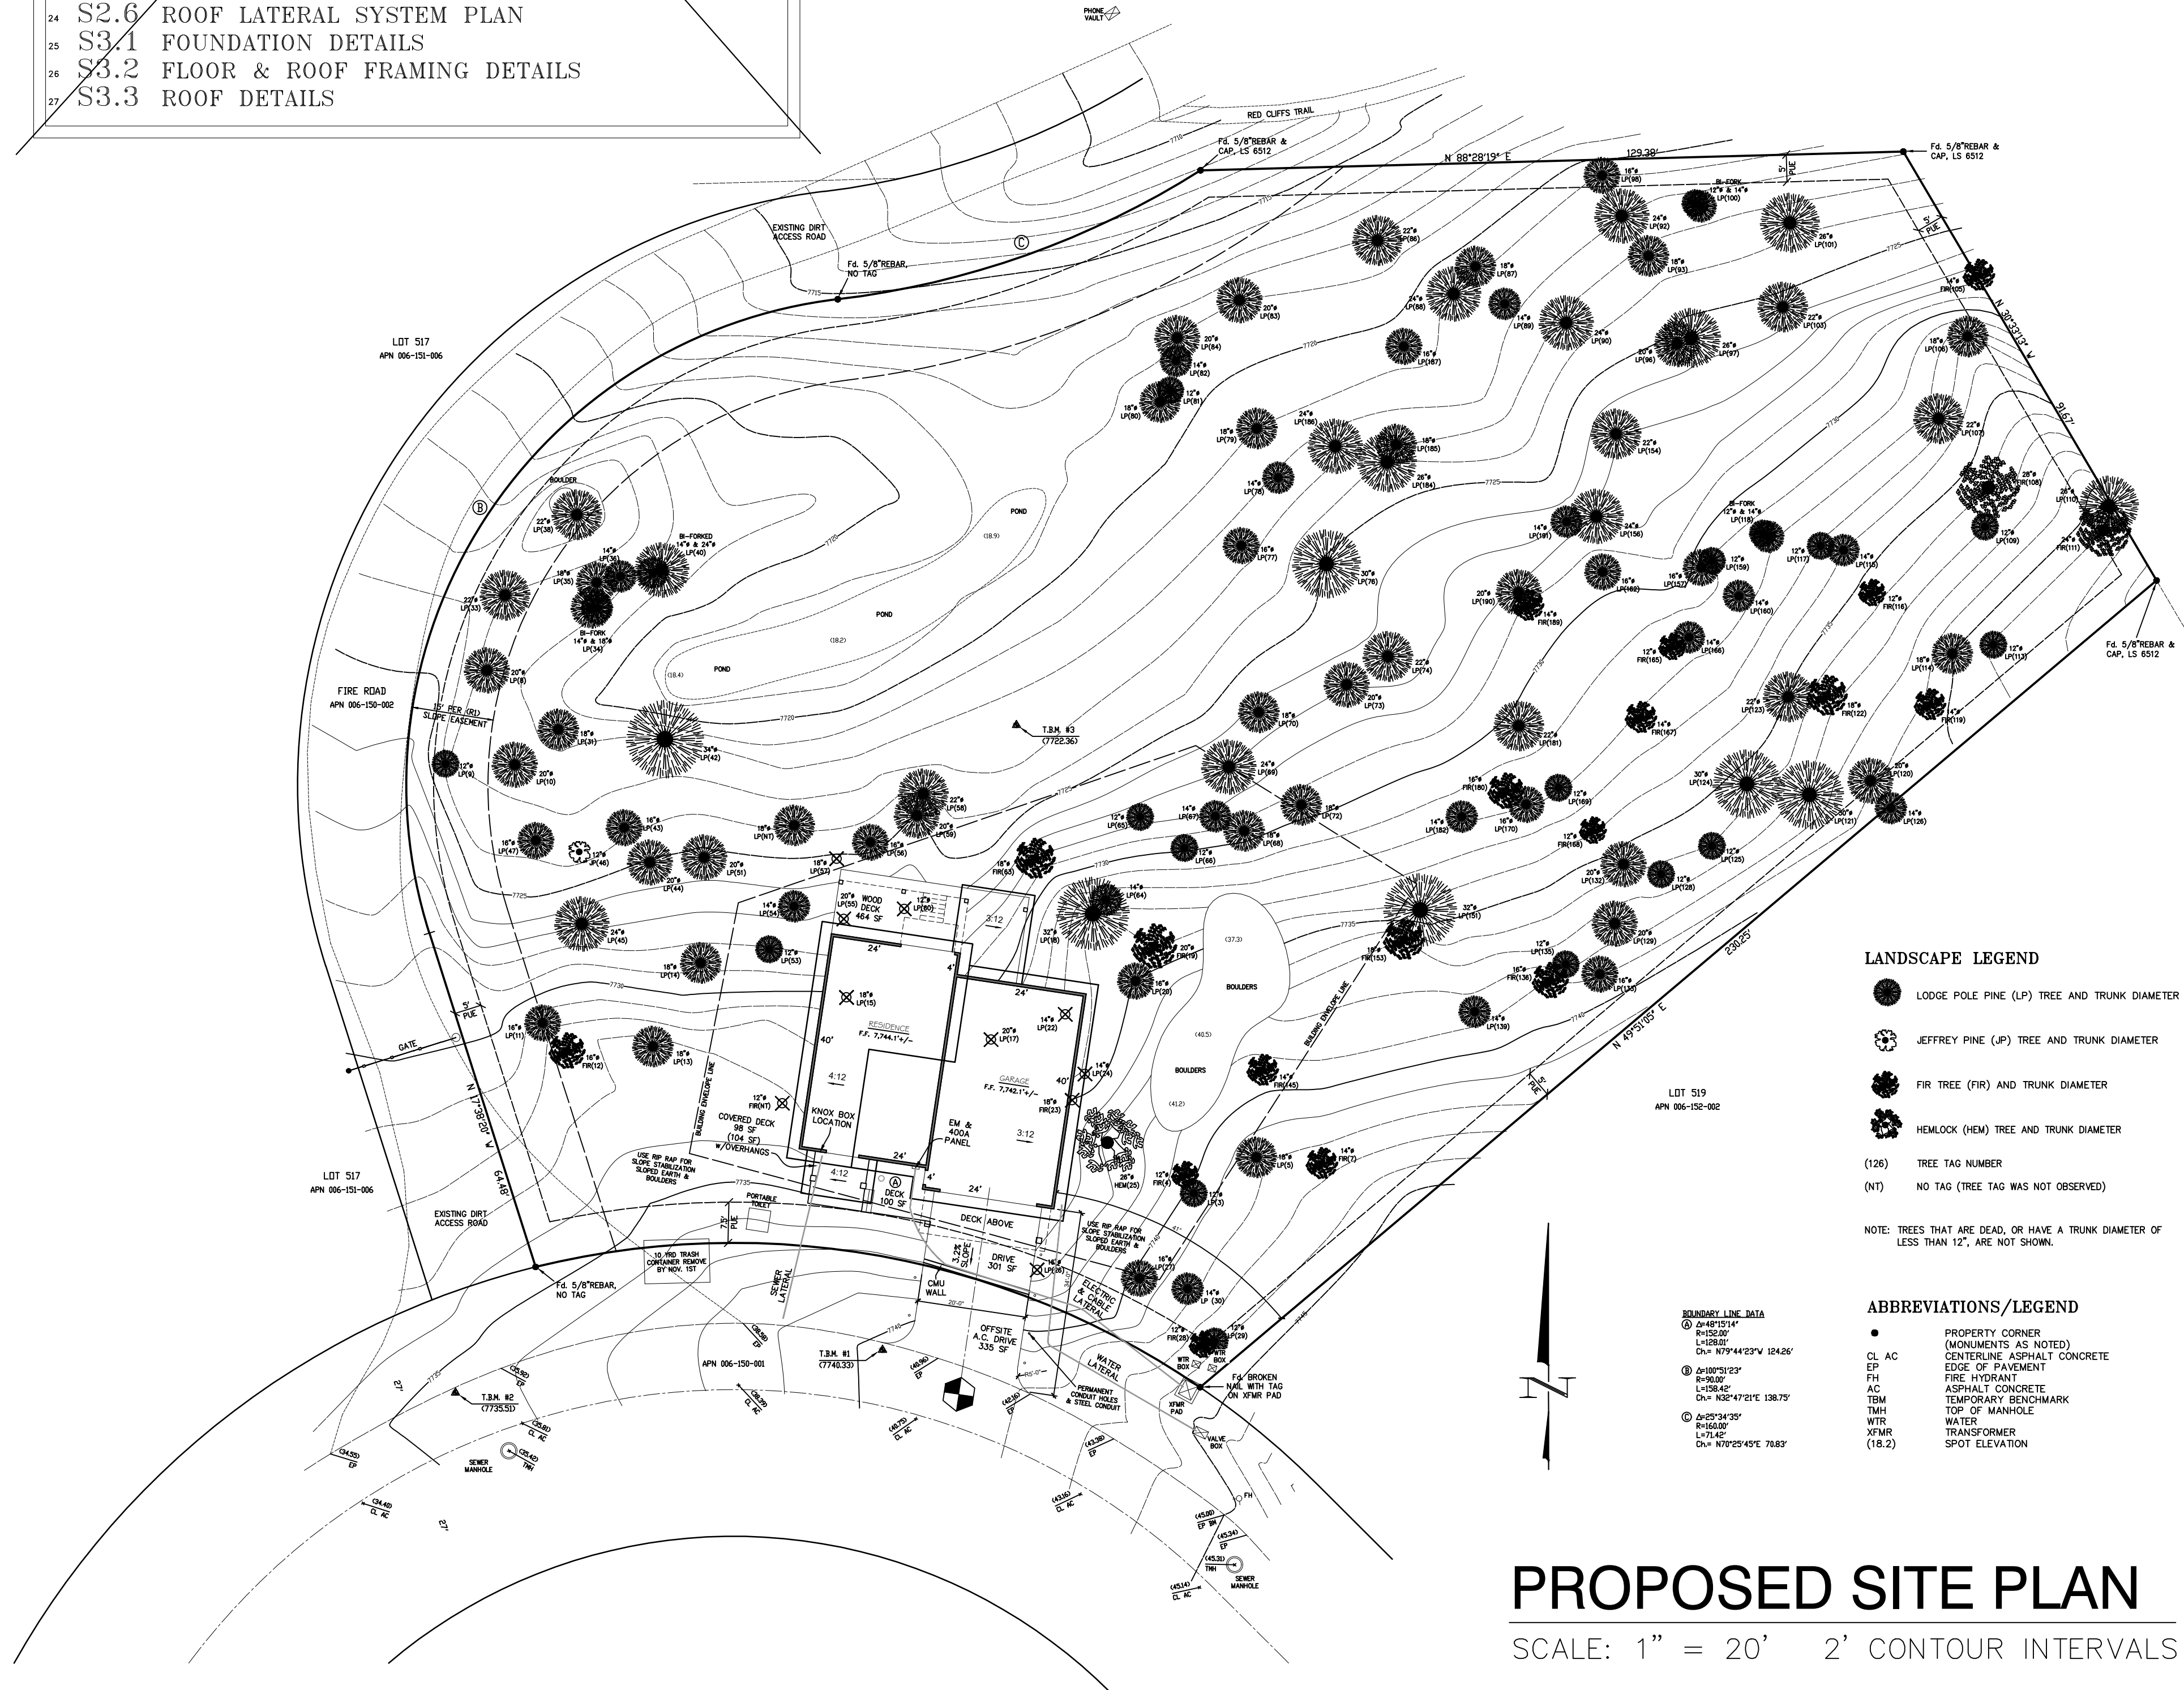

LANDSCAPE LEGEND

- LODGE POLE PINE (LP) TREE AND TRUNK DIAMETER
- JEFFREY PINE (JP) TREE AND TRUNK DIAMETER
- FIR TREE (FR) AND TRUNK DIAMETER
- HEMLOCK (HEM) TREE AND TRUNK DIAMETER


- (126) TREE TAG NUMBER
- (NT) NO TAG (TREE TAG WAS NOT OBSERVED)

NOTE: TREES THAT ARE DEAD, OR HAVE A TRUNK DIAMETER OF
LESS THAN 12", ARE NOT SHOWN.

ABBREVIATIONS/LEGEND

- CL AC PROPERTY CORNER (MONUMENTS AS NOTED)
- EP CENTERLINE ASPHALT CONCRETE
- PA EDGE OF PAVEMENT
- AC FIRE HYDRANT
- TBM ASPHALT CONCRETE
- TBM TOP OF MANHOLE
- WTR TEMPORARY BENCHMARK
- XTR WATER TRANSFORMER
- (18.2) SPOT ELEVATION

BOUNDARY LINE DATA
① 240°10'14" 154.82'
② 107°44'23" 124.25'
③ 240°51'03" 154.82'
④ 107°44'23" 124.25'
⑤ 240°51'03" 154.82'
⑥ 107°44'23" 124.25'

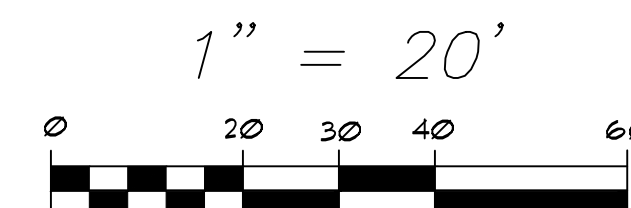

TITLE PAGE & PROPOSED SITE PLAN

PROJECT FOR:
GRIFFIN RESIDENCE
795 COLUMBINE CIRCLE LOT 518
KIRKWOOD, ALPINE COUNTY, CA 95646
APN: 006-152-001

Scale:
As Noted

Drawn By:
SB

Date:
04/09/25

Revision:

Drawing Number:

C1

ZONE 1: 0-5' NONCOMBUSTABLE AREA

CREATE A NONCOMBUSTABLE AREA AT LEAST 5 FEET WIDE AROUND THE BASE OF THE STRUCTURE (INCLUDING ALL DECKS). THIS AREA NEEDS TO HAVE A VERY LOW POTENTIAL FOR IGNITION FROM FLYING EMBERS. USE IRRIGATED HERBACEOUS PLANTS SUCH AS LAWN, GROUND COVER, AND FLOWERS THAT ARE RECOMMENDED FOR THE LAKE TAHOE BASIN; ROCK MULCHES; OR HARD SURFACES, SUCH AS BRICK AND PAVERS, IN THIS AREA.

1. THE AREA WITHIN 0-5' OF THE FOUNDATION OR SUPPORT POSTS SHOULD CONTAIN NO COMBUSTABLE MATERIALS, INCLUDING COMBUSTABLE PLANT MATERIAL. A 3" GRAVEL MOAT IS THE PREFERRED MATERIAL OF USE. DRIP LINES MAY BE INCORPORATED INTO THIS AREA.
2. REMOVE ALL PINE NEEDLES AND FOREST DUFF WITHIN THIS AREA.

ZONE 2: 5-30' LEAN, CLEAN AND GREEN AREA

FOR A DISTANCE OF 5 FEET TO 30 FEET FROM THE STRUCTURE, THERE SHOULD BE A LEAN, CLEAN, AND GREEN AREA. "LEAN" INDICATES THAT ONLY A SMALL AMOUNT OF FLAMMABLE VEGETATION, IF ANY, IS PRESENT WITHIN 30 FEET OF THE STRUCTURE. "CLEAN" MEANS THERE IS LITTLE OR NO ACCUMULATION OF DEAD VEGETATION OR FLAMMABLE DEBRIS WITHIN THE AREA DURING FIRE SEASON. "GREEN" IMPLIES THAT PLANTS LOCATED WITHIN THIS AREA ARE KEPT HEALTHY, GREEN AND IRRIGATED DURING FIRE SEASON.

1. TRIM ALL TREES OVER 20 FEET A MINIMUM OF 10 FEET ABOVE ADJACENT GRADE.
2. REMOVE ANY TREE 14 INCHES DIAMETER OR LESS (AS INDICATED ON DRAWINGS) TO CREATE A 10 FOOT SPACE BETWEEN ANY ADJACENT TREE CANOPY. REFER TO DETAIL 2.
3. REMOVE ACCUMULATION OF DEAD VEGETATION FROM TREES (FLAMMABLE DEBRIS, DEAD BRANCHES AND LIMBS) 10 FEET ABOVE ADJACENT GRADE.
4. WITHIN 5-30' OF THE STRUCTURE ONLY SINGLE SPECIMENS OF WELL MAINTAINED AND WELL IRRIGATED SHRUBS OR TREES SHOULD BE PRESENT. SUCH MATERIALS SHOULD NOT BE CAPABLE OF READILY TRANSMITTING FIRE TO THE STRUCTURE. COMBUSTABLE MULCHES OR PINE NEEDLES SHOULD NOT BE USED AS GROUND COVER WITHIN THIS ZONE.
5. ALL BRUSH, TREES OR FLAMMABLE MATERIAL WILL BE REMOVED FROM UNDER THE DRIP LINE OF RESIDENTIAL TREES OF THE TREE GROUP.
6. REMOVE ALL PINE NEEDLES AND FOREST DUFF WITHIN THIS AREA.

ZONE 3: 30-100' WILDLAND FUEL REDUCTION AREA

THE WILDLAND FUEL REDUCTION AREA LIES BEYOND THE LEAN, GREEN AREA AND OFTEN CONSISTS OF NATURALLY OCCURRING PLANTS (PINE TREES, MANZANITA, SAGEBRUSH, ETC.) WITHIN THIS AREA. REMOVE DEAD VEGETATION, INCLUDING DEAD SHRUBS, DRIED GRASS, FALLEN BRANCHES, THICK ACCUMULATION OF NEEDLES AND LEAVES ETC. THIN, DENSE STANDS OF SHRUBS AND TREES TO CREATE A SEPARATION BETWEEN THEM. REMOVING TREES MORE THAN 14" IN DIAMETER REQUIRES A PERMIT FROM THE TAHOE REGIONAL PLANNING AGENCY (TRPA) OR YOUR LOCAL FIRE PROFESSIONAL.


1. TREE CANOPIES WILL BE SPACED AT LEAST 10 FEET APART. IF TREES ARE GROUPED CLOSE ENOUGH TOGETHER AS TO ACT AS ONE UNIT, THEN ALL OTHER REQUIREMENTS MUST BE MET. REFER TO DETAIL 2.
2. BEYOND 30 FEET FROM THE STRUCTURE, BRUSH FIELDS MUST BE SPACED TO A DISTANCE EQUAL OR GREATER THAN TWO (2) TIMES THE HEIGHT OF THE BRUSH. INDIVIDUAL BRUSH PLANTS WILL NOT EXCEED 100 SQUARE FEET. REFER TO DETAIL 1.
3. PINE NEEDLES ARE ACCEPTABLE WITHIN ZONE 3 AS LONG AS THEY ARE NO THICKER THAN 2 OR 3 INCHES.

FOR SLOPED PROPERTIES, USE THE FOLLOWING STANDARDS:

TREES	SLOPE	SPACING
	0-20%	10 FEET BETWEEN EDGES OF CROWNS
	20-40%	20 FEET BETWEEN EDGES OF CROWNS
	40%-UP	30 FEET BETWEEN EDGES OF CROWNS
BRUSH	SLOPE	SPACING
	0-20%	2 X HEIGHT OF RESIDUAL BRUSH
	20-40%	4 X HEIGHT OF RESIDUAL BRUSH
	40%-UP	6 X HEIGHT OF RESIDUAL BRUSH

SEPARATION BETWEEN TREE BRANCHES
1 LOWER GROWING PLANTS

IF TREES ARE PRESENT WITHIN THE DEFENSIBLE SPACE ZONE, THERE SHOULD BE A SEPARATION BETWEEN THE LOWER GROWING VEGETATION AND THE LOWER TREE BRANCHES. VEGETATION THAT CAN CARRY FIRE BURNING IN LOW GROWING PLANTS TO TALLER PLANTS IS CALLED "LADDER FUEL." FOR LARGE TREES, THE RECOMMENDED SEPARATION FOR LADDER FUELS IS THREE TIMES THE HEIGHT OF THE LOWER VEGETATION LAYER. PRUNE BRANCHES FROM LOWER THIRD OF THE TREE HEIGHT, SHORTEN THE HEIGHT OF THE SHRUBS, OR REMOVE PLANTS. DO NOT REMOVE MORE THAN ONE-THIRD OF THE TOTAL TREE BRANCHES. WHEN THERE IS NO UNDERSTORY VEGETATION PRESENT, REMOVE LOWER TREE BRANCHES TO A HEIGHT OF AT LEAST FIVE FEET ABOVE GROUND. DURING FIRE, THIS WILL HELP PREVENT BURNING NEEDLES AND TWIGS THAT ARE LYING ON THE GROUND FROM IGNITING THE TREE. FOR SHORTER TREES, WHERE THREE TIMES THE HEIGHT OF THE LOWER VEGETATION LAYER EXTENDS BEYOND THE LOWER THIRD OF THE TREE HEIGHT, SHORTEN THE HEIGHT OF THE SHRUBS OR REMOVE PLANTS BELOW THE TREE.

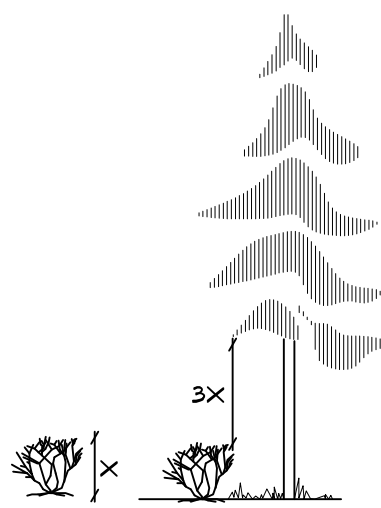

— SNOW STORAGE AREAS


DEFENSIBLE SPACE & EROSION CONTROL PLAN

SCALE: 1" = 20' 2' CONTOUR INTERVALS



1" = 20'



BMP DETAILS

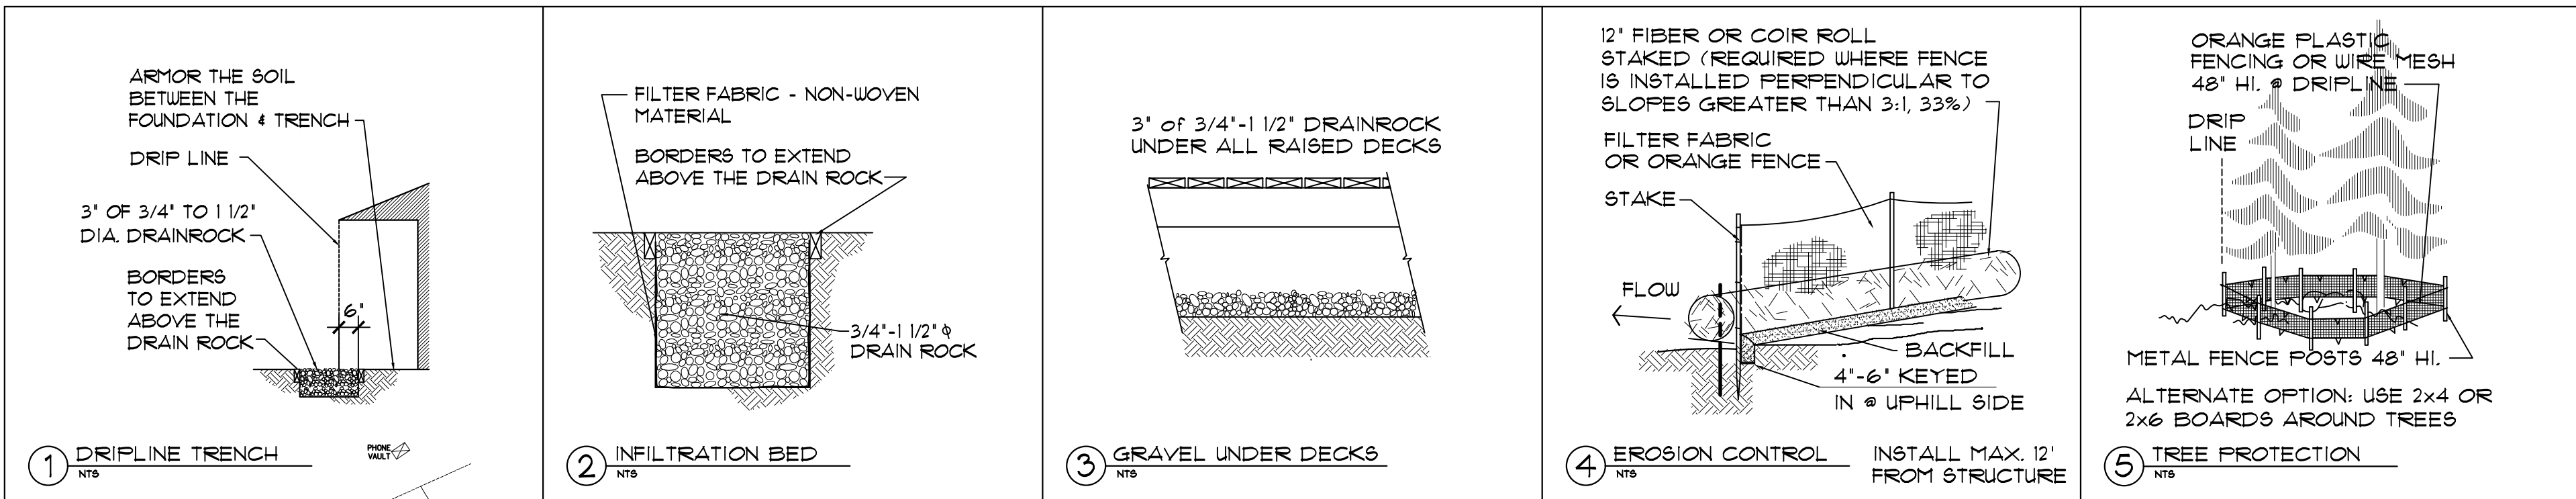


NOTE:
ALL AREAS DISTURBED BY CONSTRUCTION SHALL BE MULCHED WITH A 2 TO 3 INCH LAYER OF FINE NEEDLES OR WOOD CHIPS AS A DUST CONTROL MEASURE. THIS MULCH SHALL BE MAINTAINED FROM COMPLETION OF THE INITIAL GRADING THROUGH COMPLETION OF THE PROJECT.

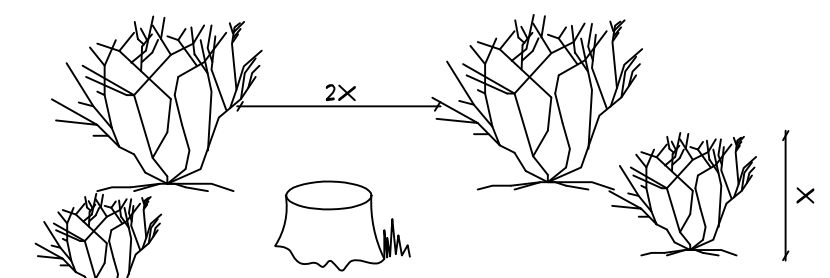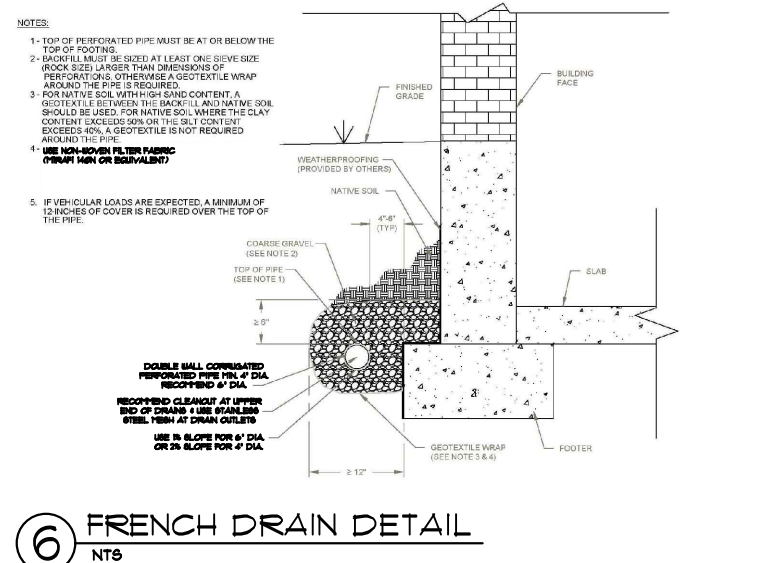

3 SEPARATION BETWEEN TREES & SHRUBS

SAGEBRUSH, MANZANITA, HUCKLEBERRY OAK, AND OTHER SHRUBS:
ON FLAT TO GENTLY SLOPING TERRAIN, INDIVIDUAL SHRUBS OR SMALL CLUMPS OF SHRUBS WITHIN THE DEFENSIBLE SPACE ZONE SHOULD BE SEPARATED FROM ONE ANOTHER BY AT LEAST TWICE THE HEIGHT OF THE AVERAGE SHRUB. FOR HOMES LOCATED ON STEEPER SLOPES, THE SEPARATION DISTANCE SHOULD BE GREATER.

FOR EXAMPLE, IF THE TYPICAL SHRUB HEIGHT IS 2 FEET, THEN THERE SHOULD BE A SEPARATION BETWEEN SHRUB BRANCHES OF AT LEAST 4 FEET. REMOVE SHRUBS OR PRUNE TO REDUCE THEIR HEIGHT AND/OR DIAMETER.

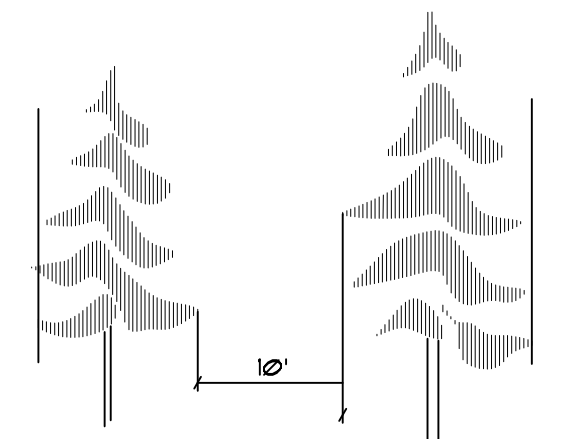

4 FOREST TREES

ON FLAT OR GENTLY SLOPING TERRAIN, TREES SHOULD BE THINNED TO PROVIDE AN AVERAGE SEPARATION BETWEEN THE CANOPIES OF AT LEAST 10 FEET (TRPA). FOR HOMES LOCATED ON STEEPER SLOPES, THE SEPARATION DISTANCE SHOULD BE GREATER. STUMPS SHOULD BE CUT SLUSH TO THE GROUND FOR TREES LESS THAN 6 INCHES IN DIAMETER AT BREAST HEIGHT, AND TO WITHIN 6 INCHES OF THE GROUND FOR LARGER TREES. THE STUMPS CUT SURFACE SHOULD BE COATED WITH POWDERED BORAX TO RETARD THE SPREAD OF ROOT DISEASES. WHEN SELECTING TREES FOR REMOVAL, CONSIDER CUTTING UNHEALTHY, DAMAGED, OR WEAK TREES. RETAIN LESS COMMON SPECIES OF TREES, SUCH AS INCENSE CEDAR, SUGAR PINE, AND WESTERN JUNIPER IF POSSIBLE.

DEFENSIBLE SPACE & EROSION CONTROL PLAN



TITLE:

PROJECT FOR:
GRIFFIN RESIDENCE
795 COLUMBINE CIRCLE LOT 518
KIRKWOOD, ALPINE, CA 95646
APN: 006-152-001

Scale:

As Noted

Drawn By:

SB


Date:

04/09/25

Revision:

Drawing Number:

C3

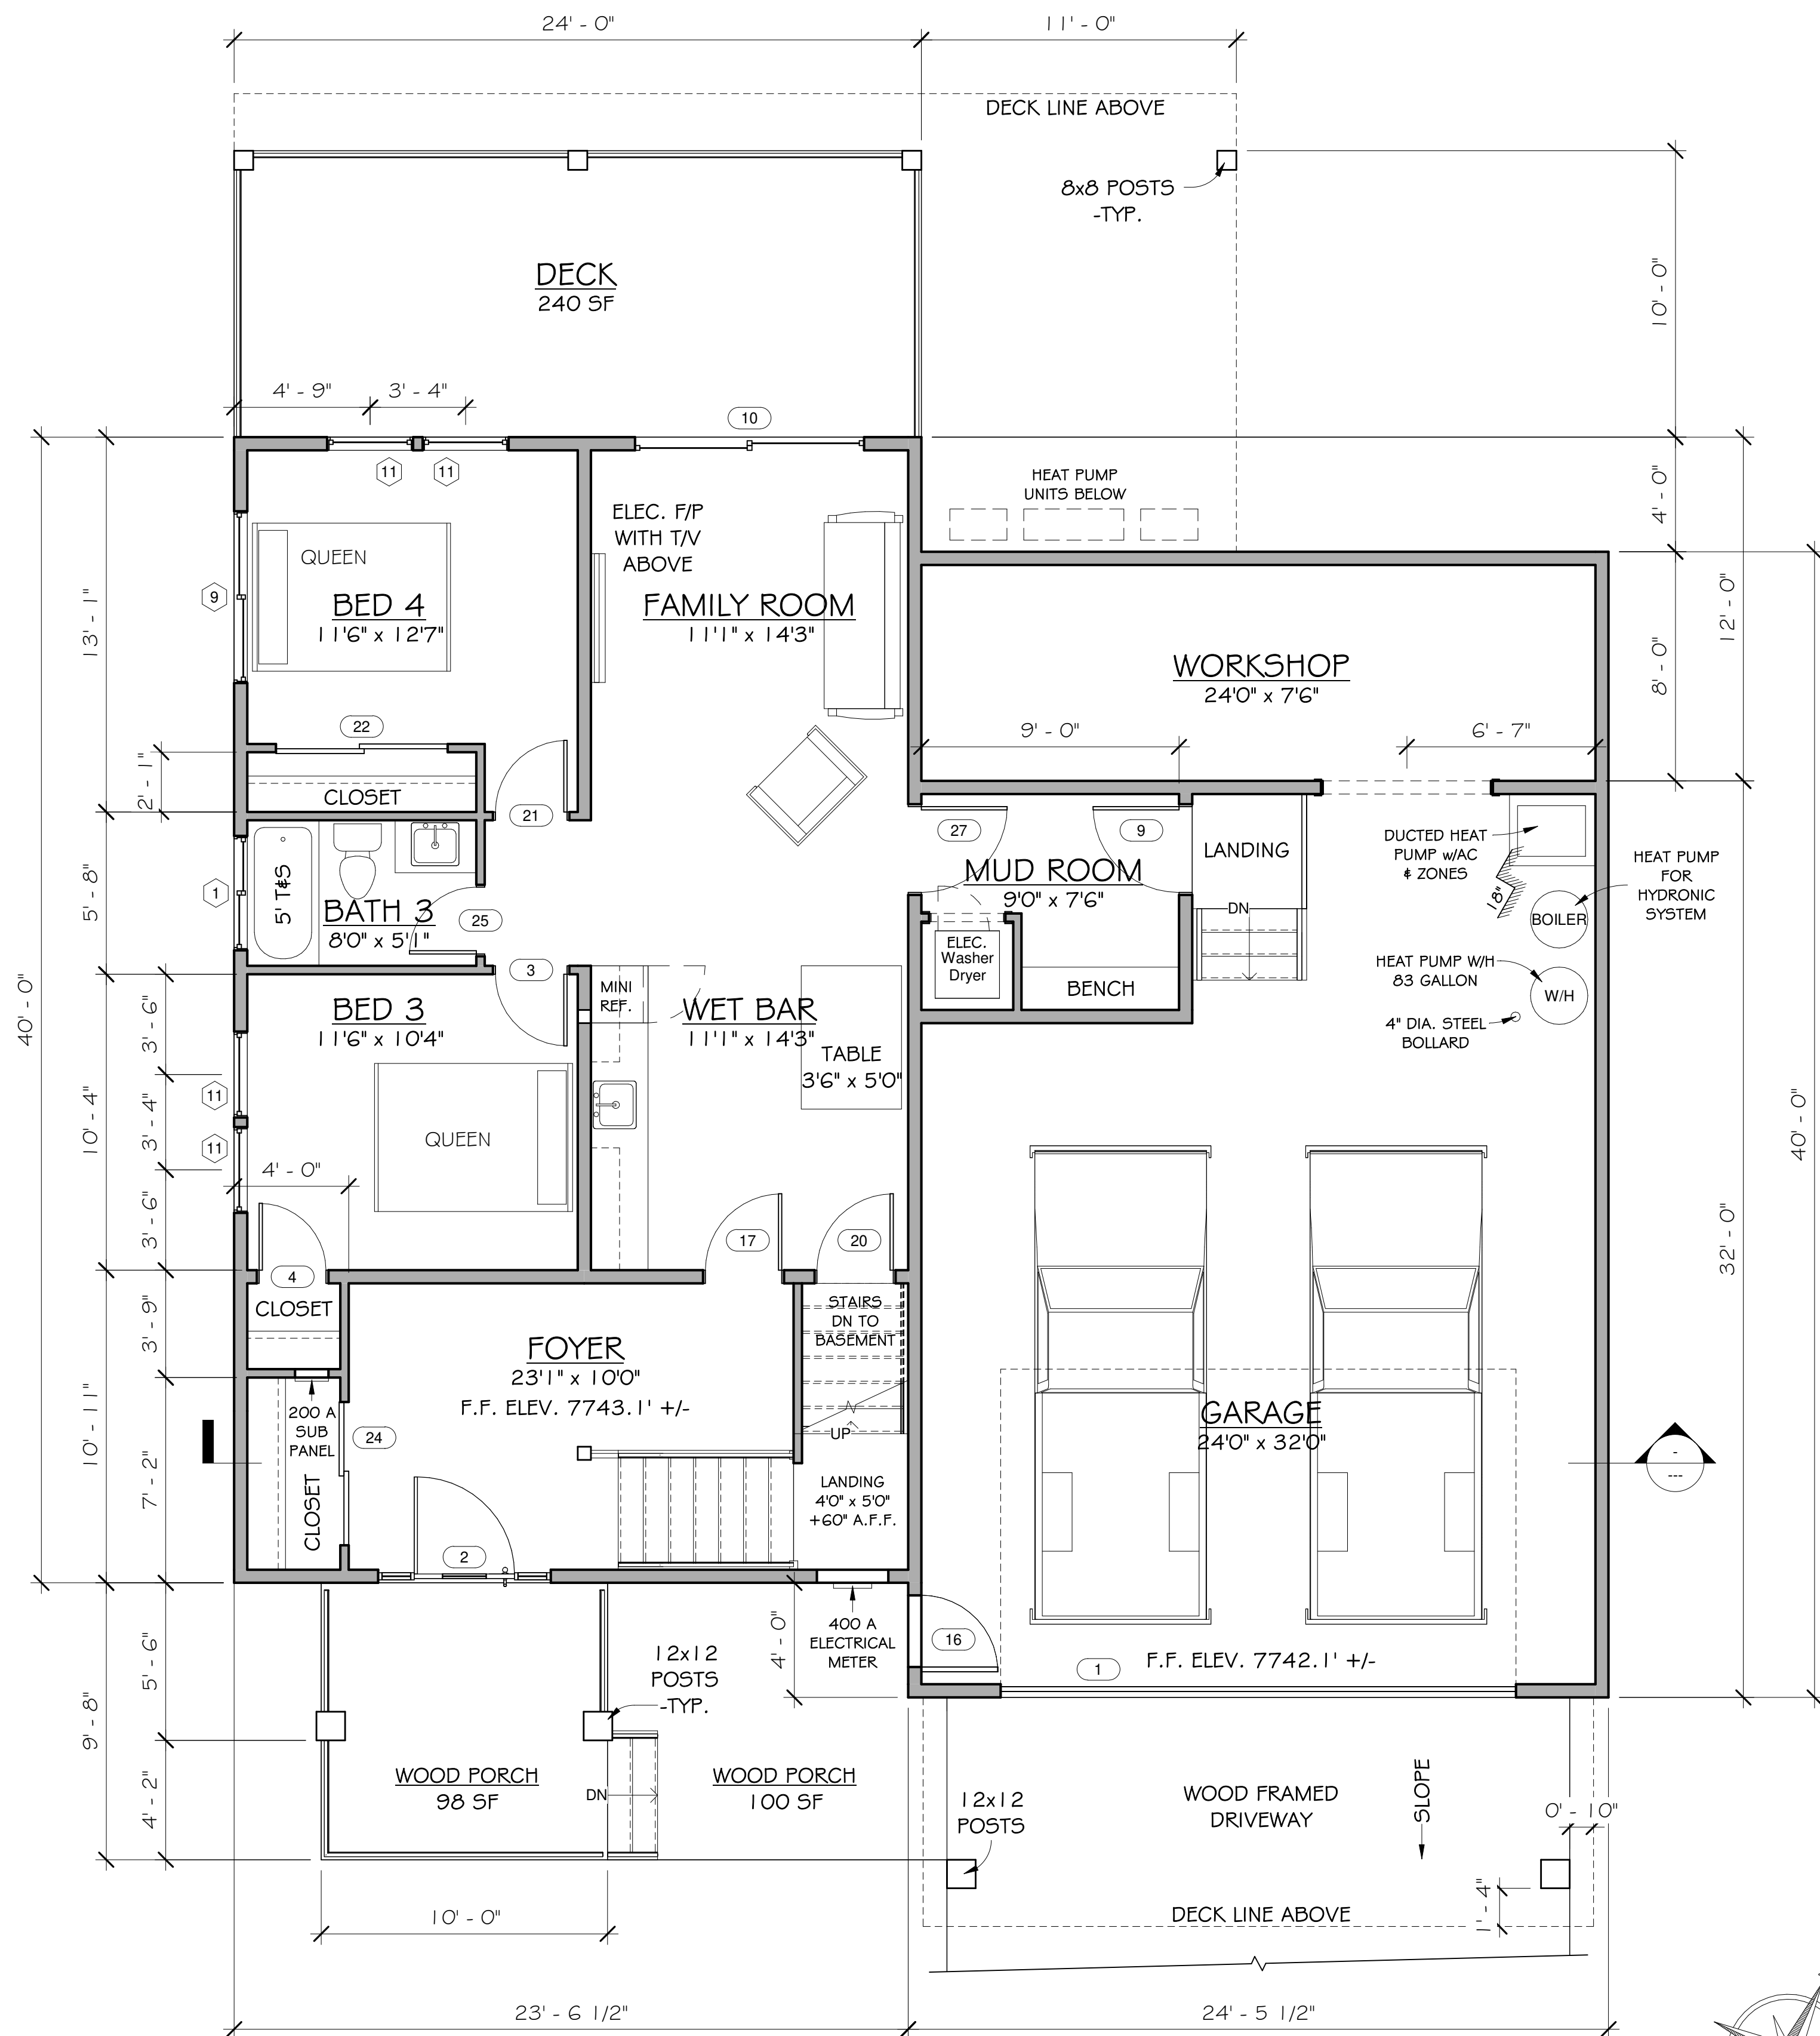


PROPOSED LOWER FLOOR PLAN

SCALE: 1/4" = 1' - 0"

NOTE: HYDRONIC HEATED FLOOR THIS LEVEL

LIVING AREA	PROPOSED
UPPER FLOOR:	1,840 SF
LOWER FLOOR:	1,040 SF
TOTAL LIVING AREA:	2,880 SF
GARAGE AREA:	887 SF
BASEMENT:	898 SF
UNCONDITIONED	

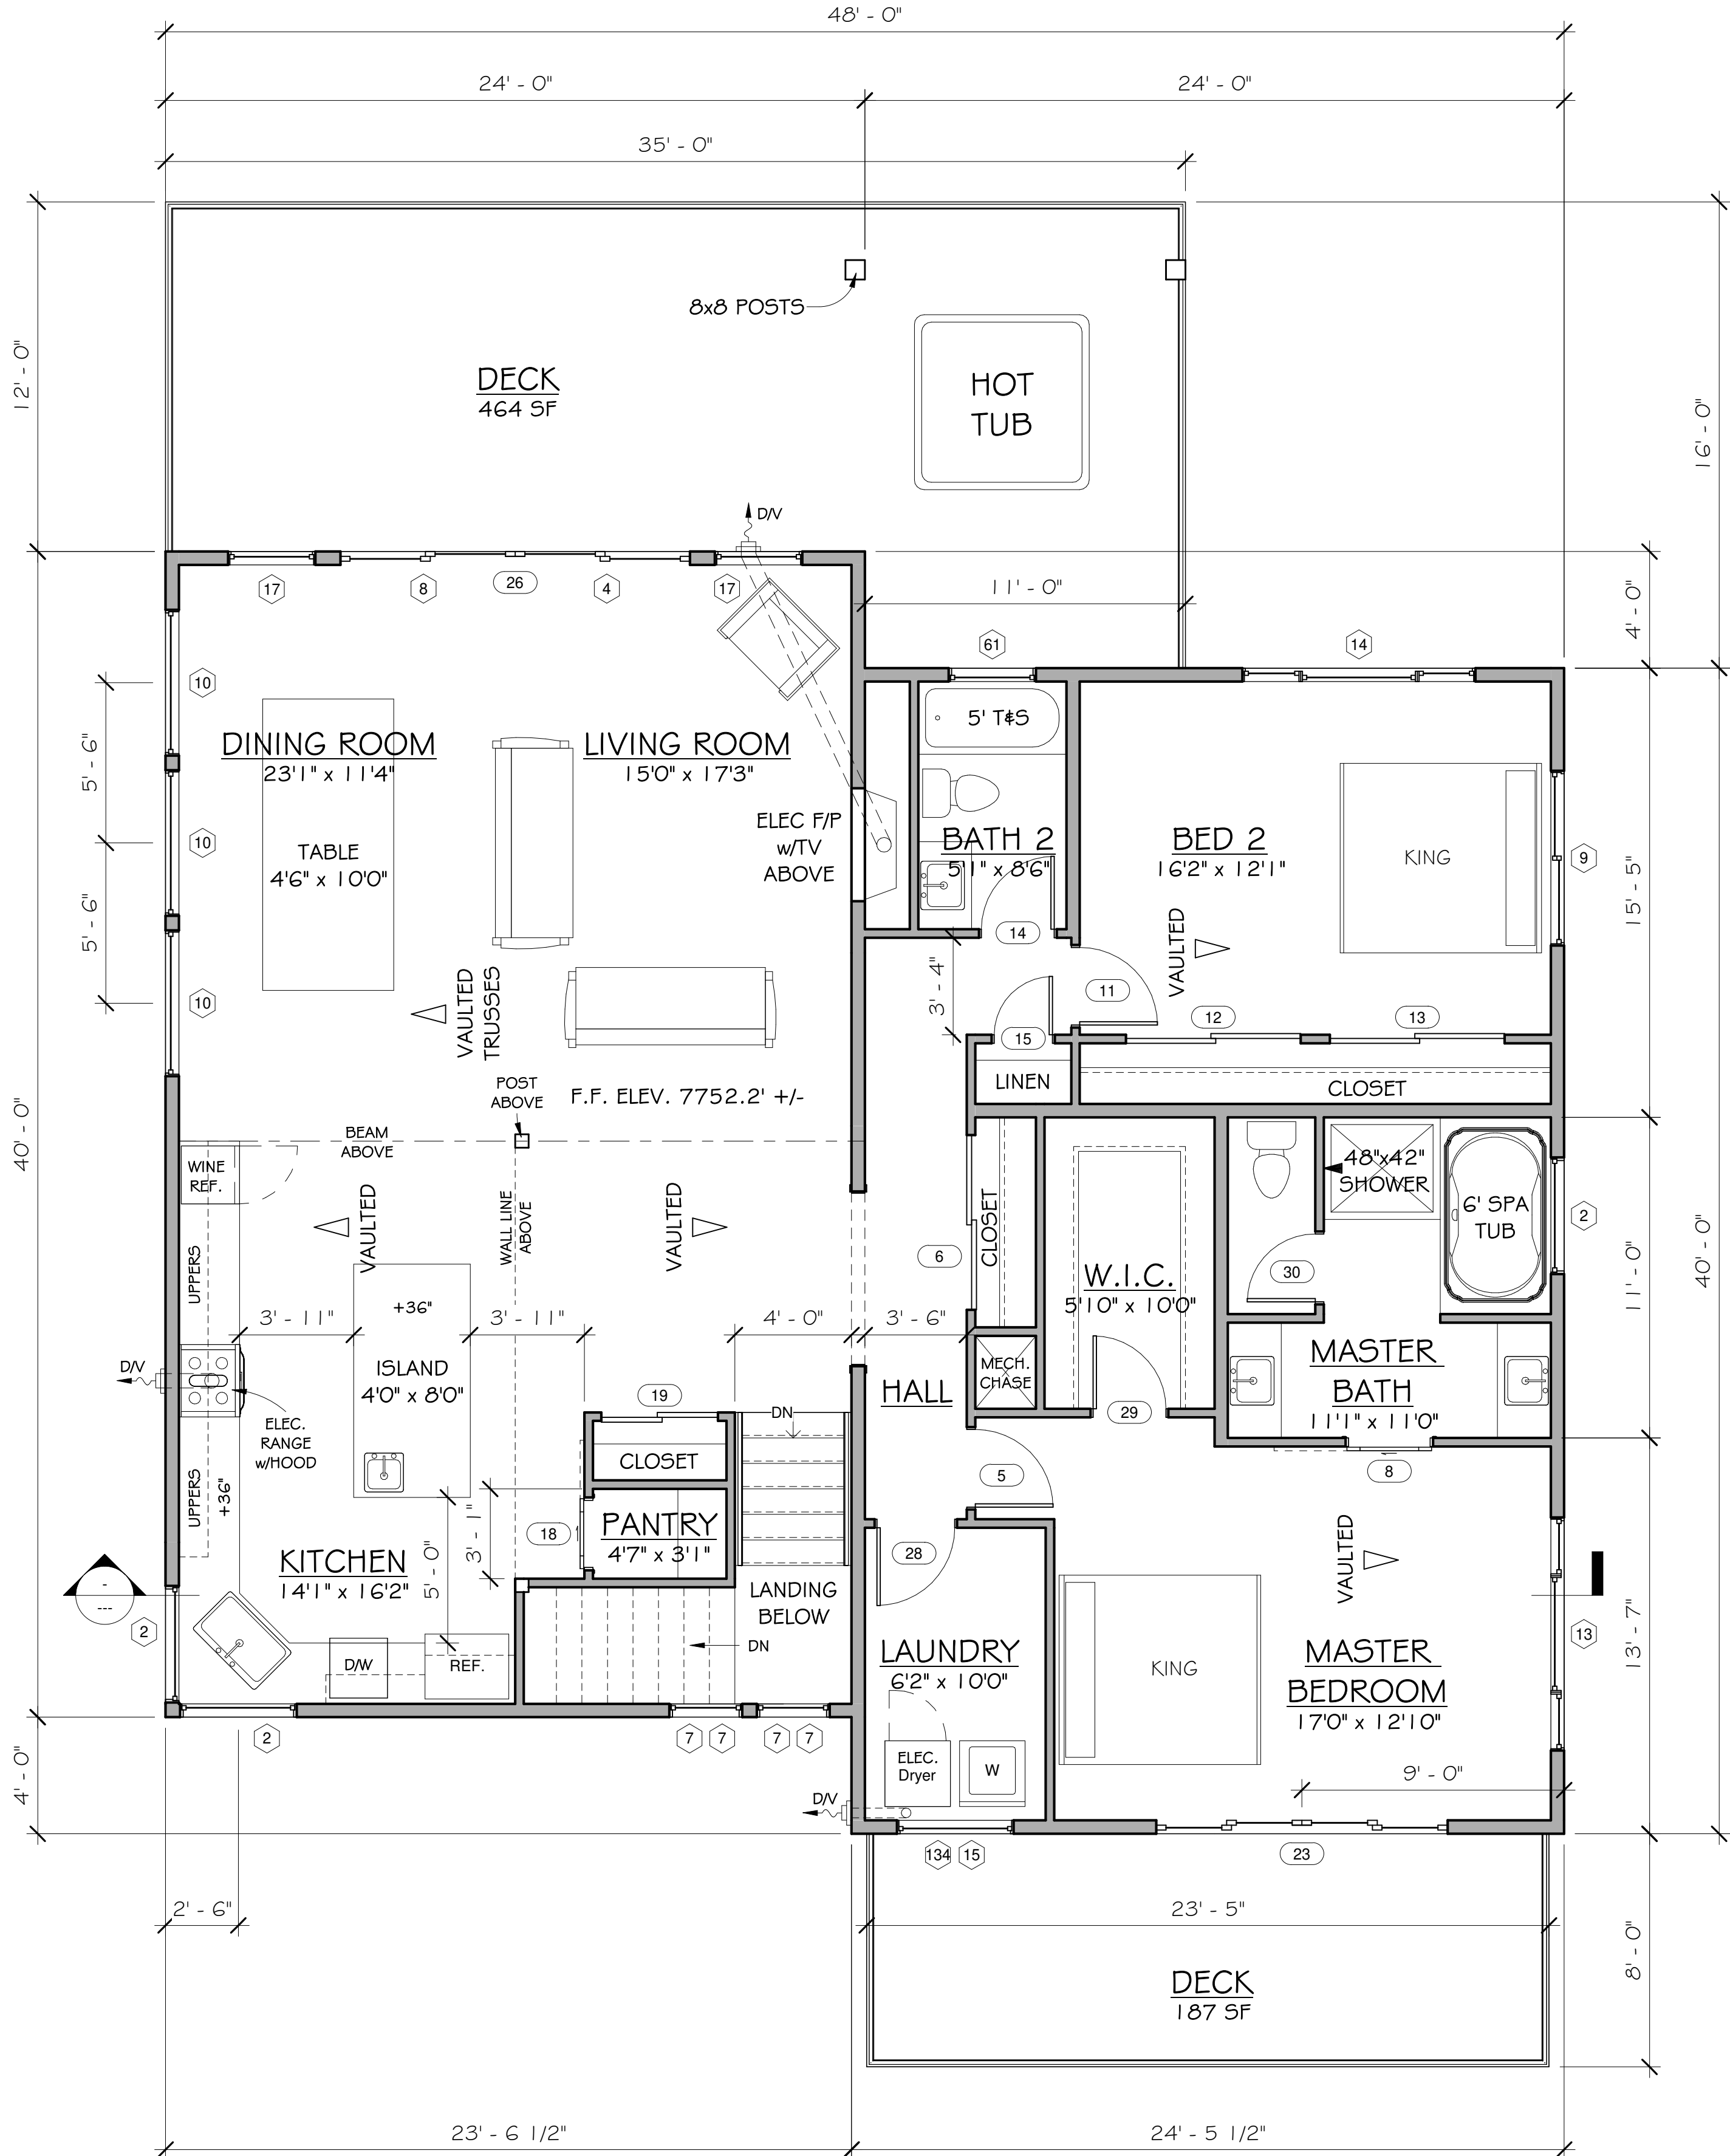

PROPOSED UPPER FLOOR PLAN


SCALE: 1/4" = 1' - 0"

NOTE:
ALL EXTERIOR WATER LINES TO BE BURIED MIN. 42" BELOW GRADE

EXTERIOR HOSE BIBS TO BE EQUIPPED WITH A BACKFLOW PREVENTION DEVICE FOR FREEZE PROTECTION

NO PLUMBING ALLOWED IN EXTERIOR WALLS. FUR OUT EXTERIOR WALLS ACCORDINGLY TO ACCOMMODATE PLUMBING

NOTE:
PLATE HEIGHTS - 8'0" -TYP.
HDR HEIGHTS - 7'0" -TYP. (SEE SCHEDULES)
2x6 EXT. WALLS -TYP. U.N.O.
2x4 INT. WALLS -TYP. U.N.O.
WINDOWS DBL PANE COMPOSITE / BLACK -TYP.
TRUSSED & STACKED ROOF SYSTEMS
HVAC TO USE ZONES

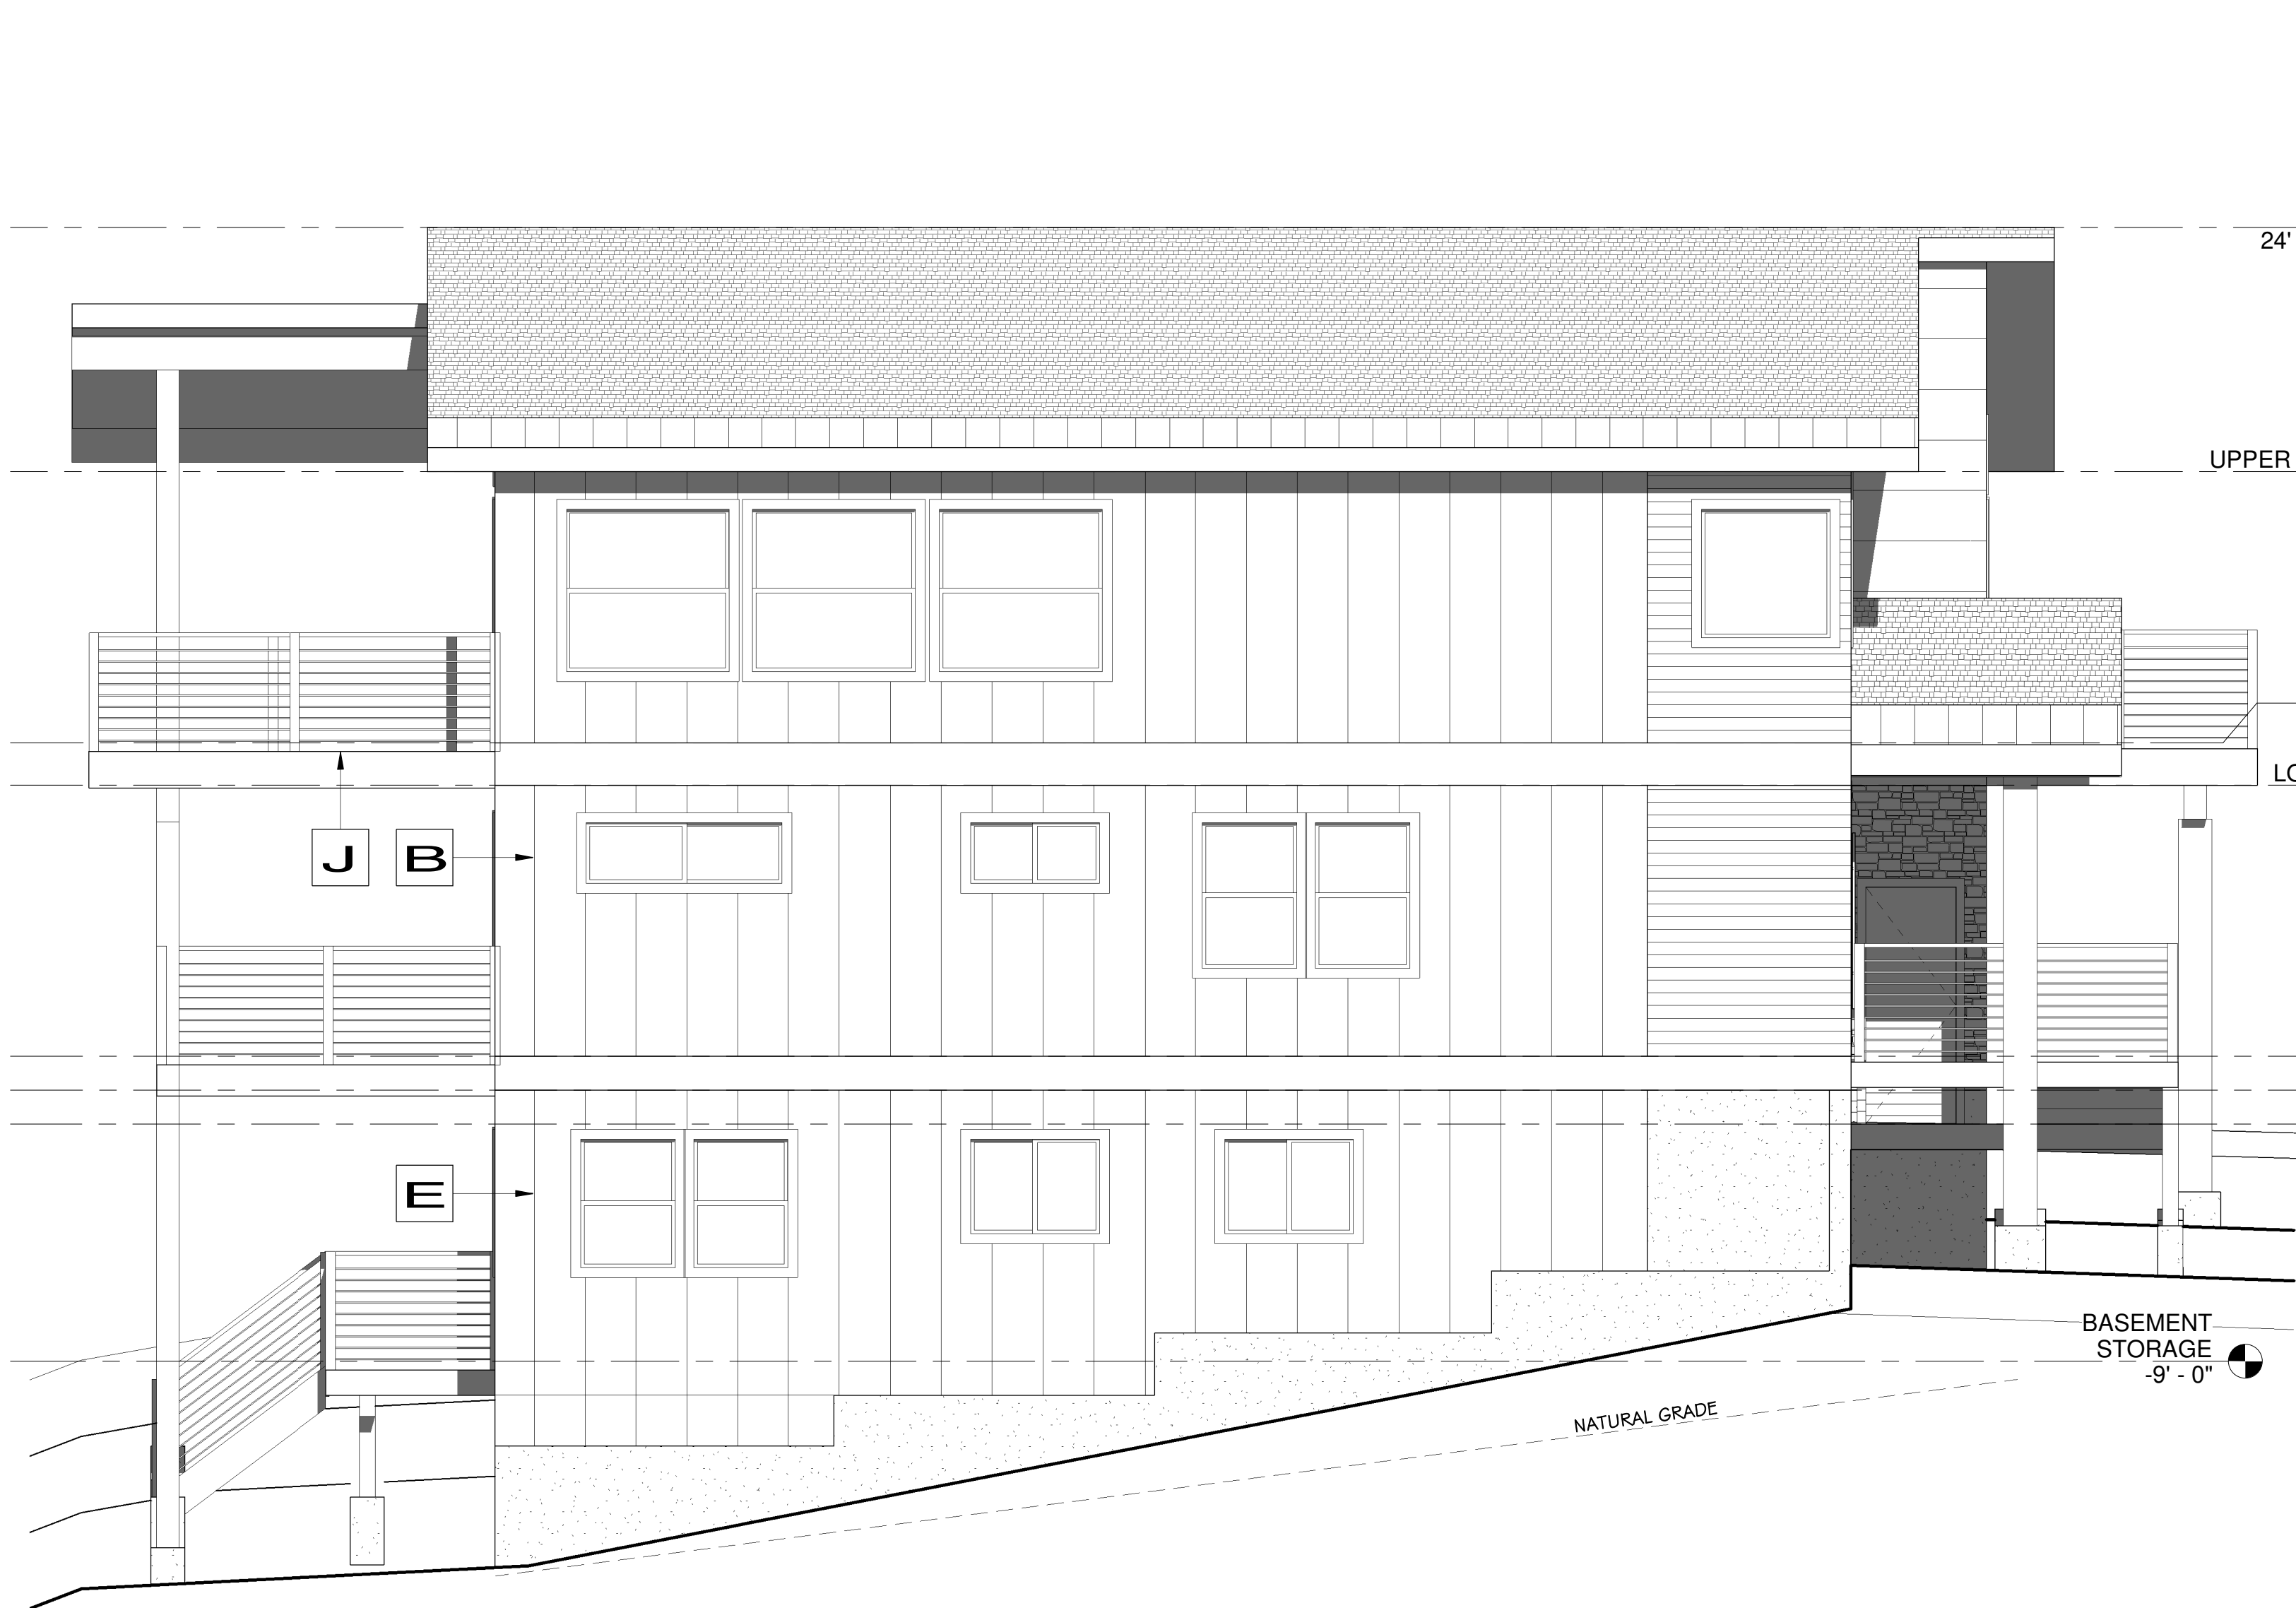

PROPOSED LEFT ELEVATION

SCALE: 1/4" = 1' - 0"

EXTERIOR MATERIALS				
A	LANDMARK PRO BY CERTAIN-TEED ASPHALT COMPOSITION ROOF 40 YR MIN. RECOMMEND 50 YR	CLASS "A" COMP. GREY W/ICE & WATER SHIELD AS REQ'D	G	DUAL GLAZED WINDOWS
B	18" VERTICAL SIDING NICHHA FIBER CEMENT	OVER HOUSEWRAP & 1/2" SHEATHING INDUSTRIAL BLOCK - GREY	H	DOOR/WINDOW & CORNER TRIM CEDAR PLANK
C	18" HORIZONTAL SIDING NICHHA FIBER CEMENT	OVER HOUSEWRAP & 1/2" SHEATHING RIFTSAWN - CHESTNUT	I	FASCIA BD. W/SHINGLE MOULDING CEDAR PLANK
D	6" HORIZONTAL SIDING NICHHA FIBER CEMENT	OVER HOUSEWRAP & 1/2" SHEATHING ROUGHSAWN - ESPRESSO	J	COMPOSITE DECKING (TO MEET CBC WUI / CRC R337.9.3)
E	STUCCO - 3 COAT	OVER HOUSEWRAP & 1/2" SHEATHING GREY	K	GARAGE DOOR
F	NATIVE GRANITE STONE	AS SHOWN BROWN/GREY	L	METAL ROOFING 3 TO 4" UP ALL OVERHANGS (V.I.F.)

THE EXPOSED UNDERSIDE OF EXTERIOR PORCH CEILINGS (INCLUDING OPEN & ENCLOSED ROOF EAVES) * WOOD SIDING SHALL BE A NON-COMBUSTIBLE OR IGNITION-RESISTANT MATERIAL, OR FIRE RETARDANT TREATED WOOD. PER CRC R337.7.4/5/6

FOR DECK FRAMING WEATHERPROOFING USE VOC COMPLIANT STAIN

EXTERIOR HANDRAILINGS TO BE HOG PANELS DRILLED INTO POSTS MIN. 1". MAXIMUM 4" OPENINGS.

SIDING SHALL NOT BE IMITATION ROCK
NO CROSS BRACING AT DECKS

1) SNOW CRICKETS SHALL BE INSTALLED ON ALL PLUMBING VENTS ON SLOPED ROOFS, 26 GA. MIN. G.I. STEEL VENTING THROUGH BARGE RAFTER PERMITTED IF PRE-APPROVED BY BUILDING DEPT. AIR ADMITTANCE VALVES REQUIRE PRIOR APPROVAL BY BUILDING OFFICIAL

2) ROOF TO HAVE A HOT OR COLD UNDERLAYMENT FROM EAVE TO 4FT. ABOVE THE EXTERIOR WALL OR TO THE RIDGE, WHICHEVER IS LESS.

3) MATERIALS & CONSTRUCTION METHODS SHALL COMPLY WITH 2022 CRC, SECTION R337.

4) ALL METAL ROOFING SHALL BE OF NON-GLARE EARTHTONE COLORS THAT MINIMIZE REFLECTIVITY, AND SHALL MEET THE MUNSSELL COLOR VALUE SET FORTH IN APPENDIX G OF THE DESIGN REVIEW GUIDELINES WITH A VALUE AND CHROMA OF 0-4.

Proposed Door Schedule		
Door Number	Door Size	Comments

1	Adjustable garage door _with windows_ 216" x 102"	
2	42" x 96" Entry door with sidelites	
3	30" x 84"	
4	28" x 84"	
5	32" x 84"	
6	72" x 84"	
7	36" x 80"	
8	3 vision pannels	
9	36" x 84"	
10	96" x 84"	
11	32" x 84"	
12	72" x 80"	
13	72" x 80"	
14	30" x 84"	
15	24" x 84"	
16	32" x 84"	
17	32" x 84"	
18	3 vision pannels	
19	48" x 84"	
20	32" x 84"	
21	30" x 84"	
22	72" x 84"	
23	120" x 84"	
24	60" x 84"	
25	28" x 84"	
26	144" x 84"	
27	36" x 84"	
28	32" x 84"	
29	30" x 84"	
30	28" x 84"	

Grand total: 30

Proposed Window Schedule						
Type Mark	Rough Opening		Type	Head Height	Sill Height	Comments
	Width	Height				

1	4' - 0"	2' - 0"	Slider with Trim	7' - 0"	5' - 0"	
2	4' - 0"	4' - 0"	Fixed with Trim	7' - 0"	3' - 0"	
2	4' - 0"	4' - 0"	Fixed with Trim	7' - 0"	3' - 0"	
2	4' - 0"	4' - 0"	Fixed with Trim	7' - 0"	3' - 0"	
2	6' - 0"	4' - 0"	Slider with Trim	6' - 8"	2' - 8"	
2	4' - 0"	4' - 0"	Slider with Trim	6' - 8"	2' - 8"	
4	5' - 11"	3' - 2"	Fixed_Window_with_Trim_-_Angle_top_7307	10' - 11"	7' - 9"	
5	4' - 0"	3' - 0"	Slider with Trim	6' - 8"	3' - 8"	
5	4' - 0"	3' - 0"	Slider with Trim	6' - 8"	3' - 8"	
7	2' - 6"	6' - 0"	Fixed with Trim	15' - 0"	9' - 0"	
7	2' - 6"	6' - 0"	Fixed with Trim	11' - 6"	5' - 6"	
7	2' - 6"	6' - 0"	Fixed with Trim	15' - 0"	9' - 0"	
7	2' - 6"	6' - 0"	Fixed with Trim	11' - 6"	5' - 6"	
8	5' - 11"	1' - 10 5/8"	Fixed_Window_with_Trim_-_Angle_top_7307	9' - 7 5/8"	7' - 9"	
9	6' - 0"	2' - 0"	Slider with Trim	7' - 0"	5' - 0"	
9	6' - 0"	2' - 0"	Slider with Trim	7' - 0"	5' - 0"	
10	5' - 0"	5' - 0"	Single Hung with Trim	7' - 0"	2' - 0"	
10	5' - 0"	5' - 0"	Single Hung with Trim	7' - 0"	2' - 0"	
10	5' - 0"	5' - 0"	Single Hung with Trim	7' - 0"	2' - 0"	
11	3' - 0"	4' - 6"	Single Hung with Trim	7' - 0"	2' - 6"	
11	3' - 0"	4' - 6"	Single Hung with Trim	7' - 0"	2' - 6"	
11	3' - 0"	4' - 6"	Single Hung with Trim	7' - 0"	2' - 6"	
11	3' - 0"	4' - 6"	Single Hung with Trim	7' - 0"	2' - 6"	
13	8' - 0"	4' - 0"	Picture-Side Double Hungs w Trim	7' - 0"	3' - 0"	
14	8' - 0"	5' - 0"	Picture-Side Double Hungs w Trim	7' - 0"	2' - 0"	
15	4' - 0"	4' - 0"	Single Hung with Trim	7' - 0"	3' - 0"	
16	3' - 0"	4' - 0"	Single Hung with Trim	6' - 8"	2' - 8"	
16	3' - 0"	4' - 0"	Single Hung with Trim	6' - 8"	2' - 8"	
17	3' - 0"	5' - 0"	Single Hung with Trim	7' - 0"	2' - 0"	
17	3' - 0"	5' - 0"	Single Hung with Trim	7' - 0"	2' - 0"	
61	3' - 0"	2' - 0"	Awning with Trim	7' - 0"	5' - 0"	
134	4' - 0"	2' - 0"	Fixed with Trim	9' - 6"	7' - 6"	

Grand total: 32

EMACC HEIGHT CALCULATION
PROPOSED AVG. HEIGHT: 35' - 8"
(ABOVE NATURAL GRADE)
PROPOSED AVG. HEIGHT: 32' - 11"
(ABOVE PROPOSED GRADE)
MAX. ALLOWED AVG. HEIGHT: 35' - 0"

PROPOSED FRONT ELEVATION

SCALE: 1/4" = 1' - 0"

TITLE:

PROPOSED HOUSE ELEVATIONS

PROJECT FOR:
GRIFFIN RESIDENCE
795 COLUMBINE CIRCLE LOT 518
KIRKWOOD, ALPINE CO. CA 95646
APN: 006-152-001

REVISION:


JA DESIGNS
ALL RIGHTS RESERVED

ALL DRAWINGS AND WRITTEN MATERIAL
HEREIN ARE THE PROPERTY OF JA DESIGNS
AND THE USER SHALL NOT REPRODUCE, COPIY, OR
USE, OR DISCLOSED WITH OUT THE WRITTEN
CONSENT OF JA DESIGNS

JOB No:
DRAWN BY: SB
CHECKED BY:
DATE PREPARED: 2026
SCALE: as noted
FILE:


DRAWING No:

A2

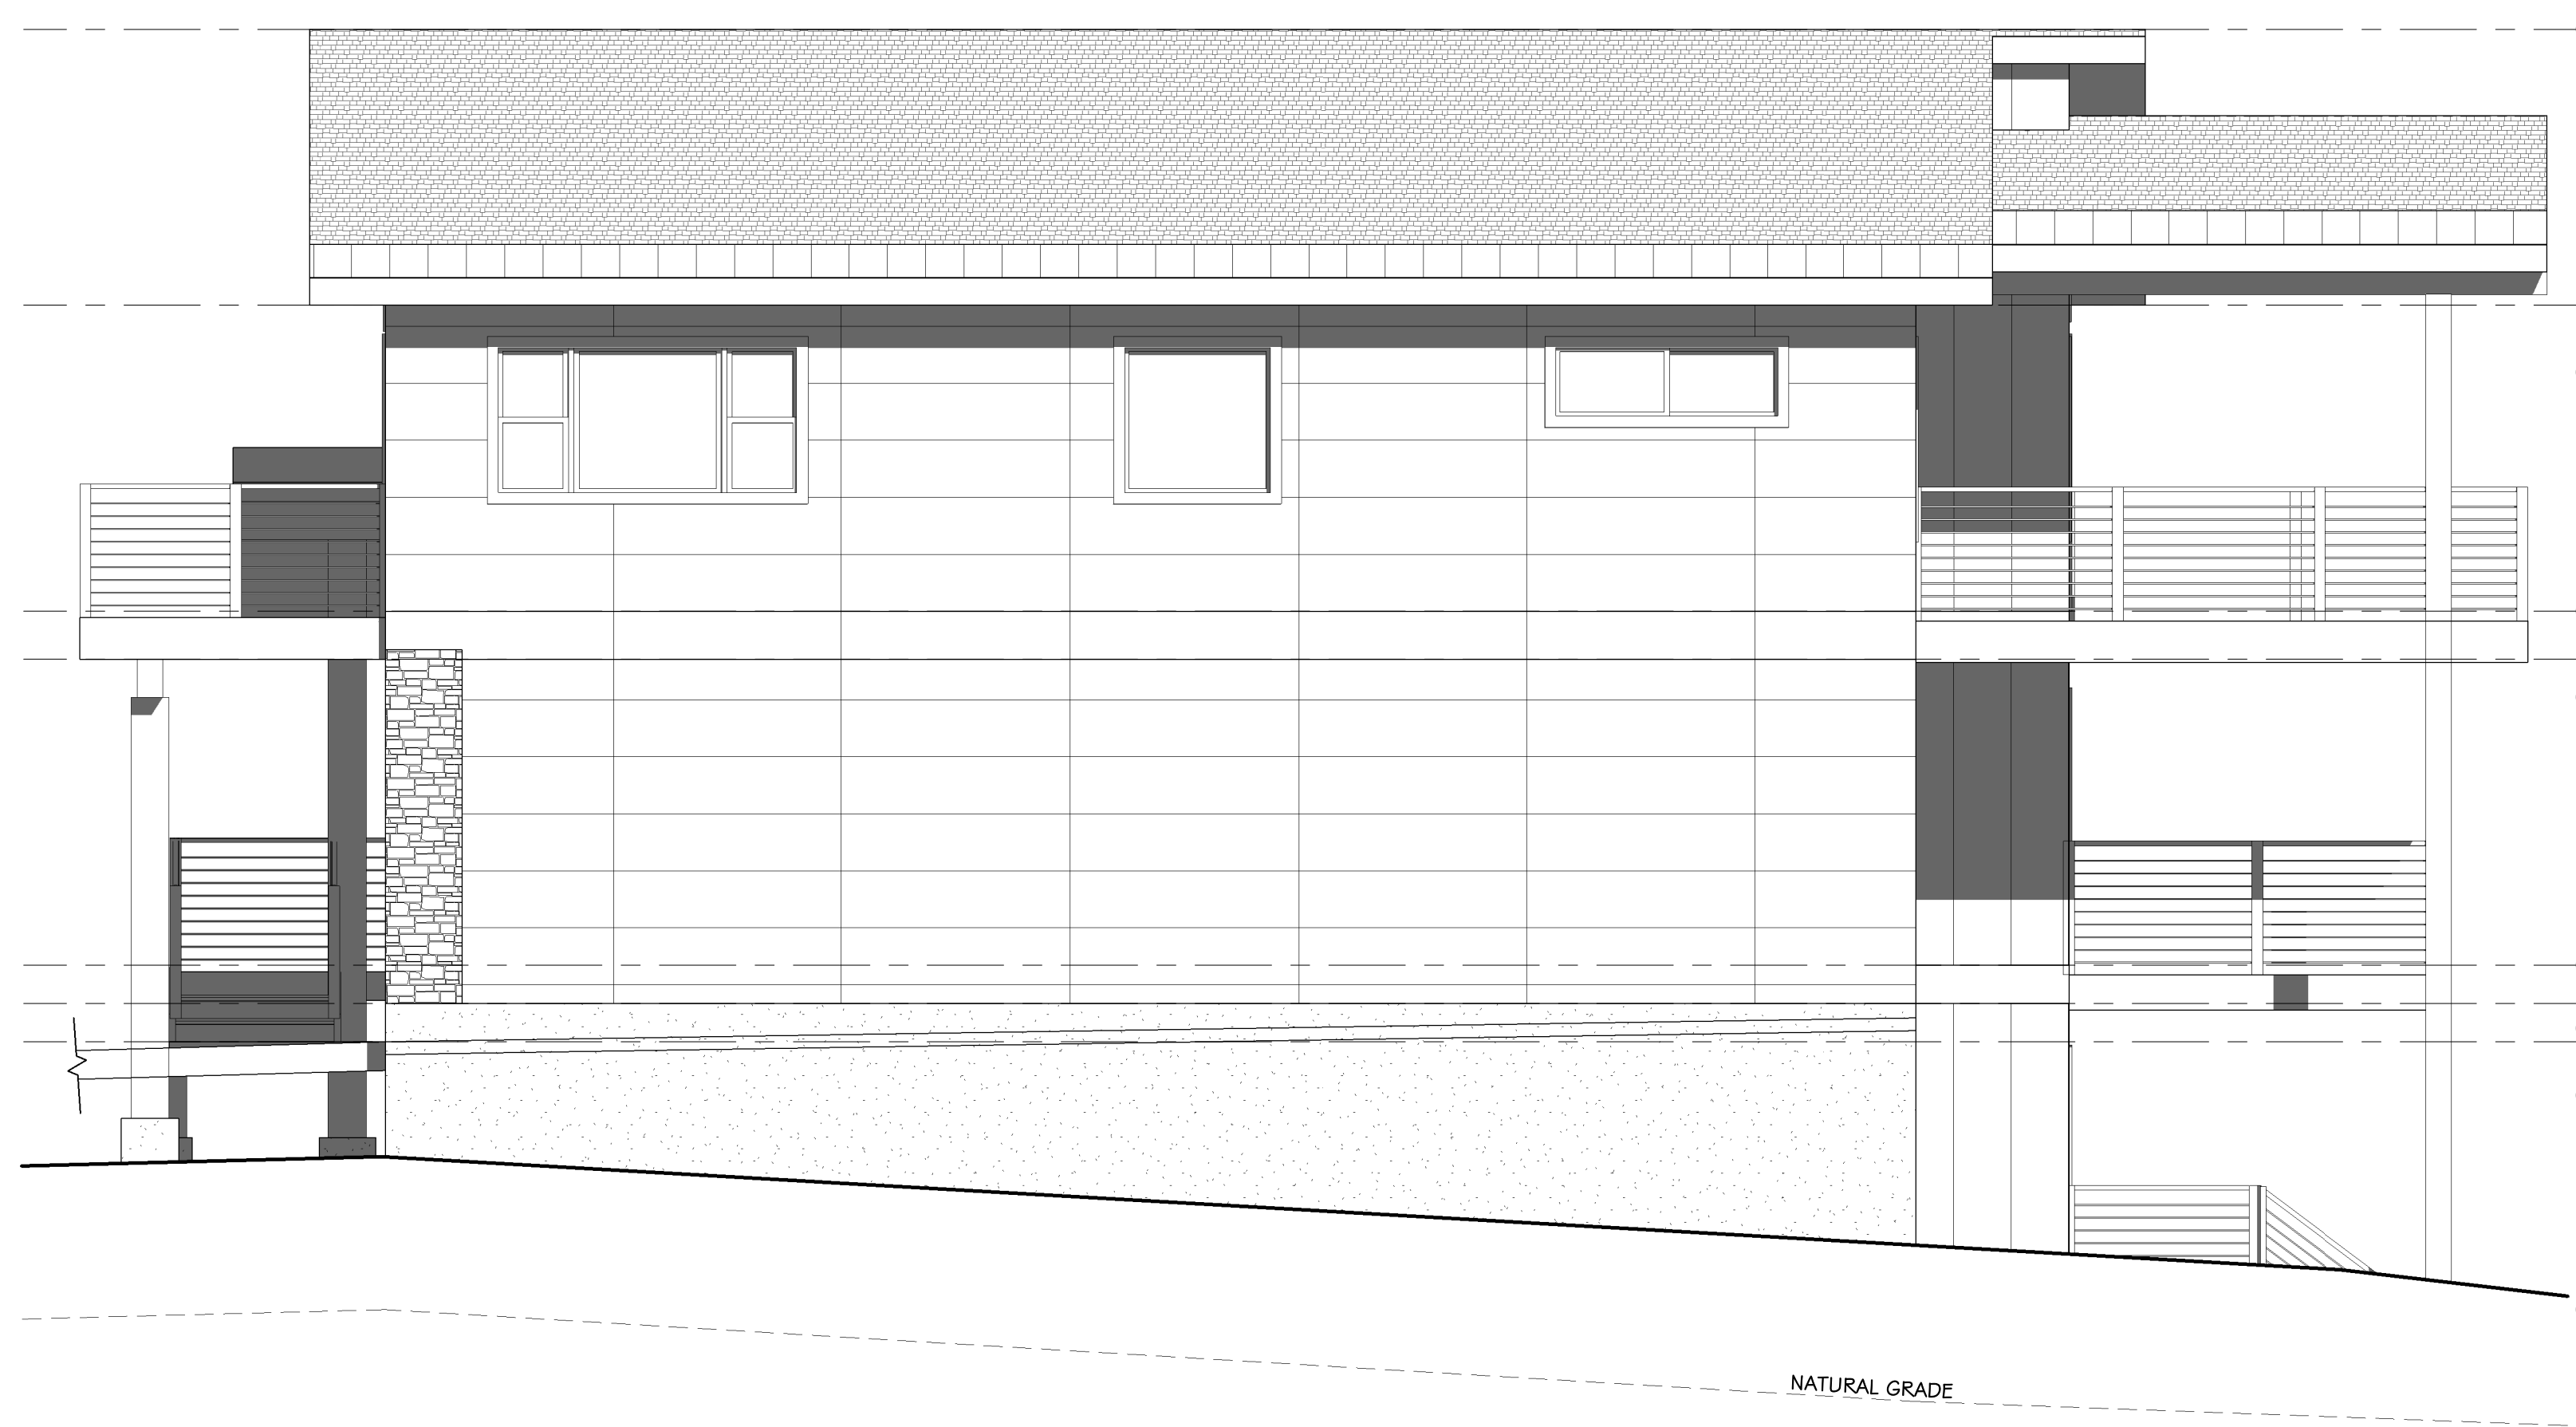





PROPOSED RIGHT ELEVATION

SCALE: 1/4" = 1' - 0"

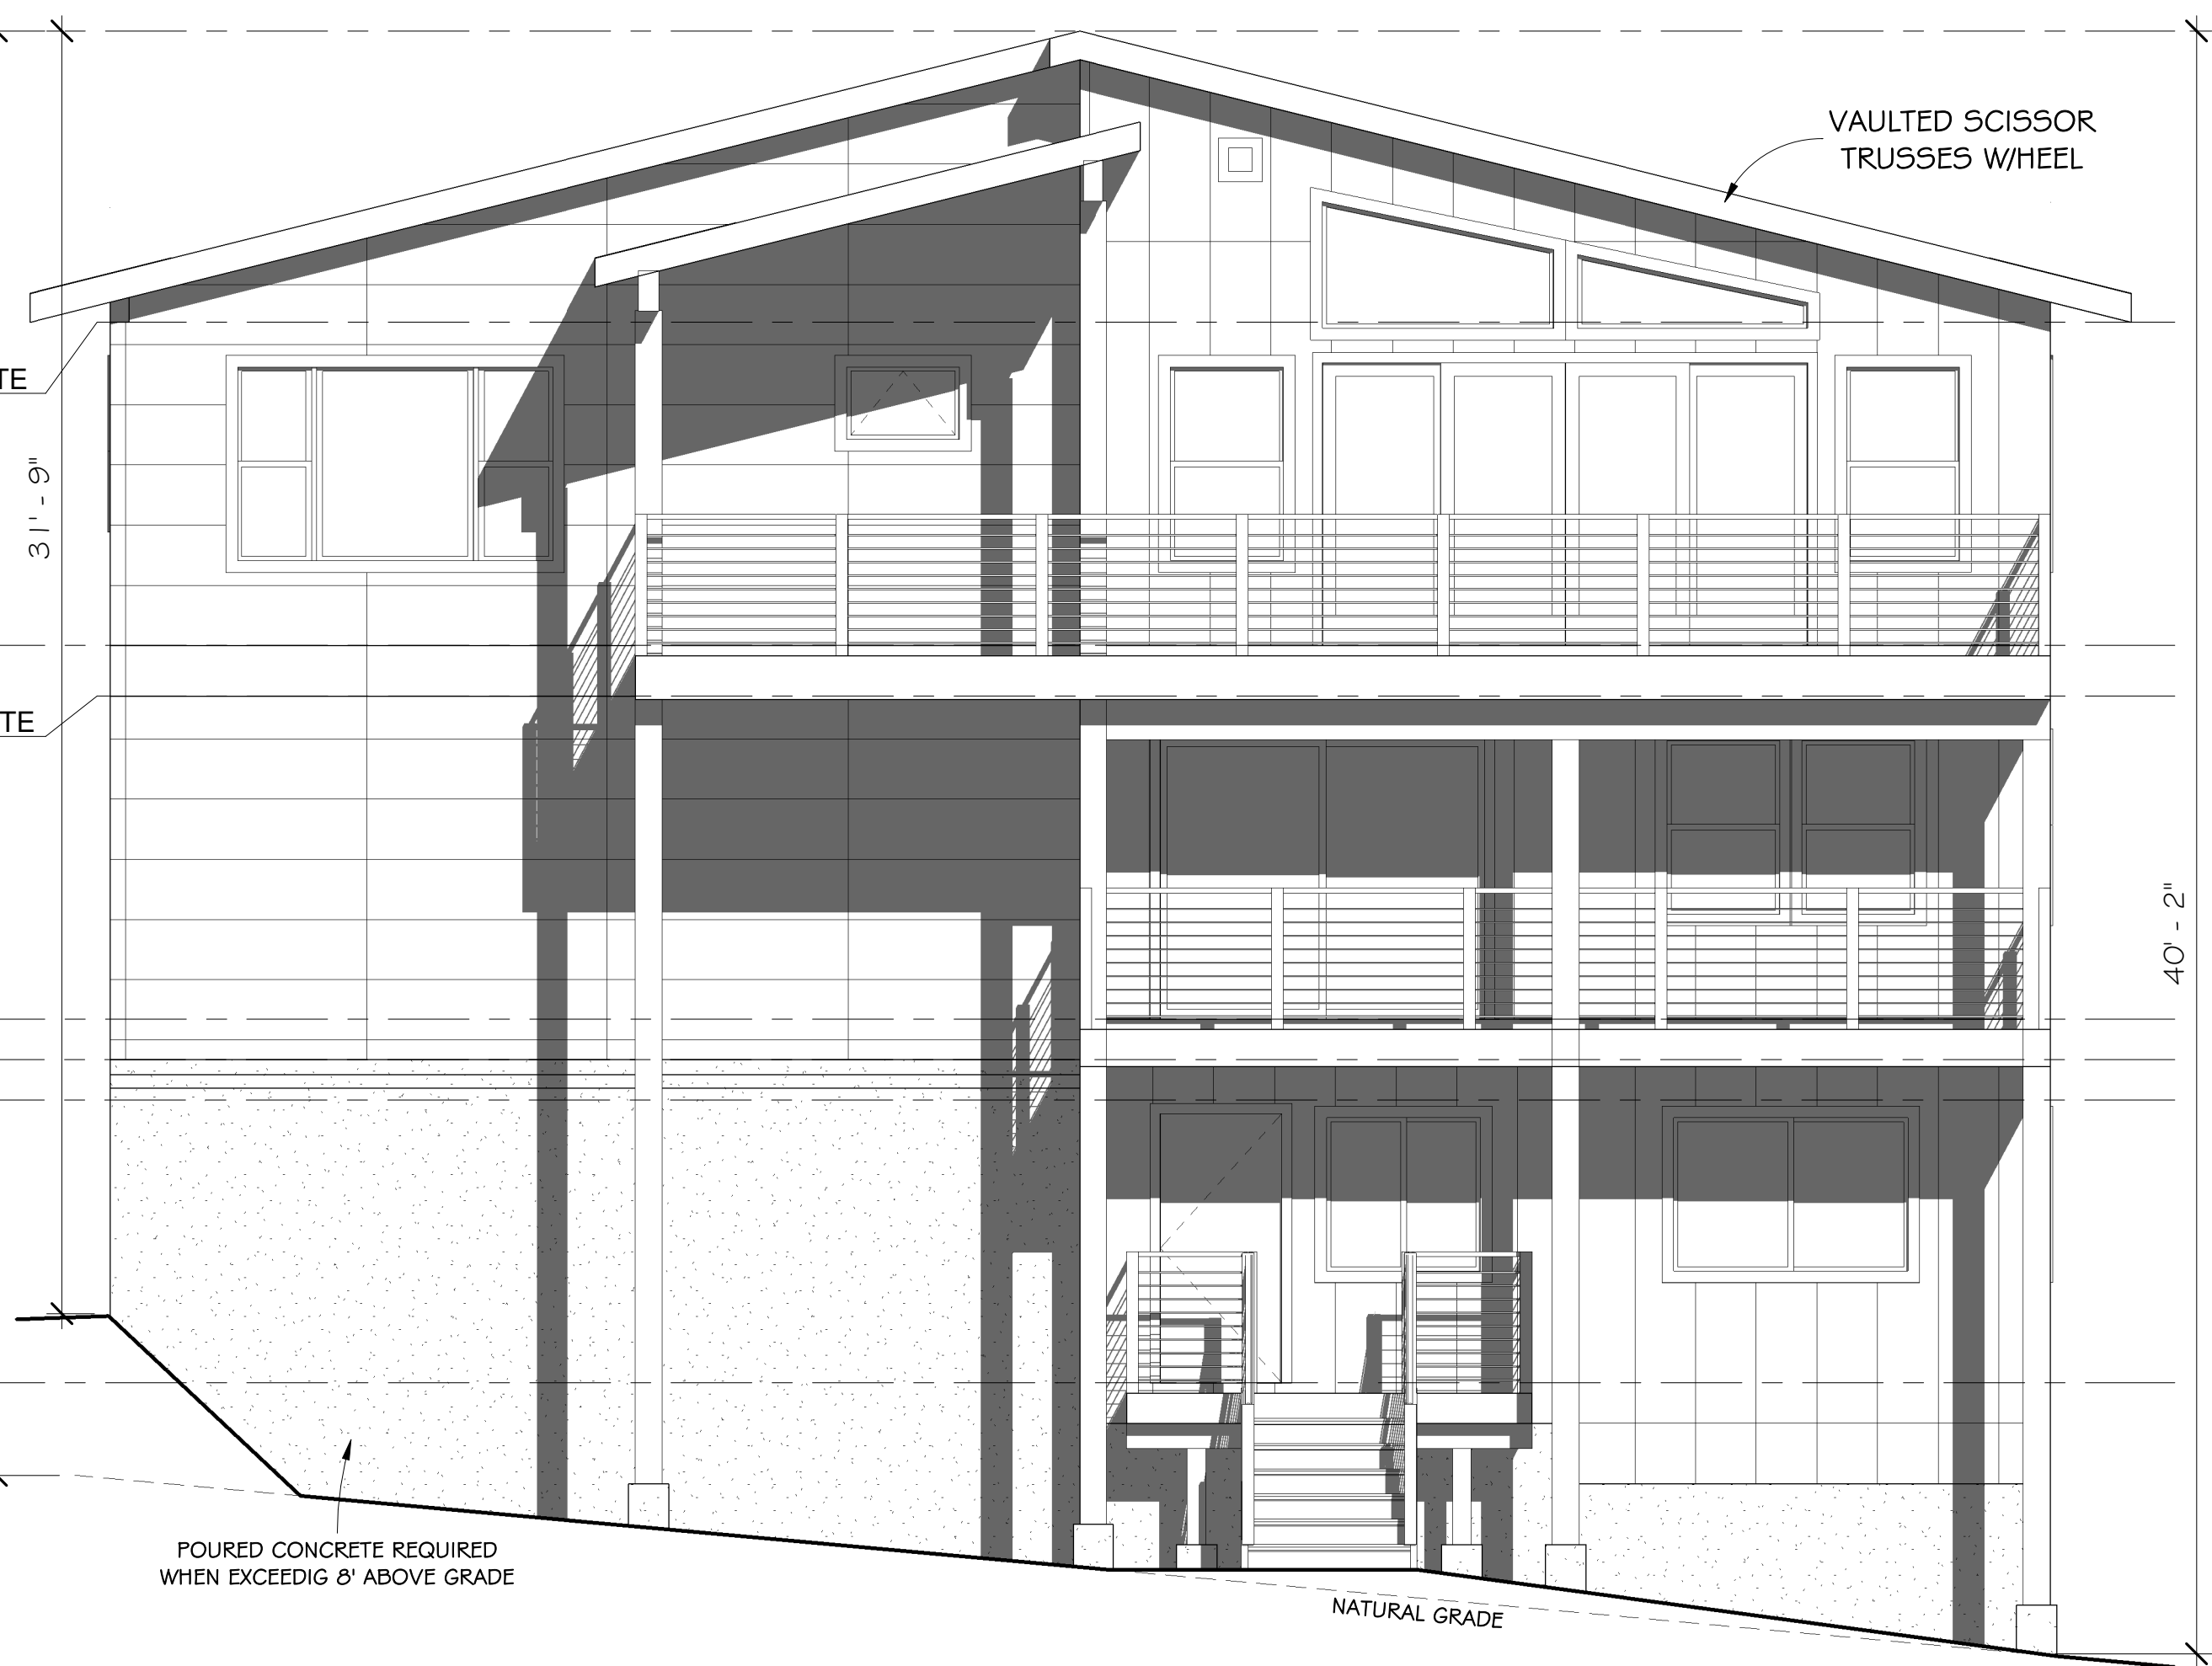

PROPOSED REAR ELEVATION

SCALE: 1/4" = 1' - 0"

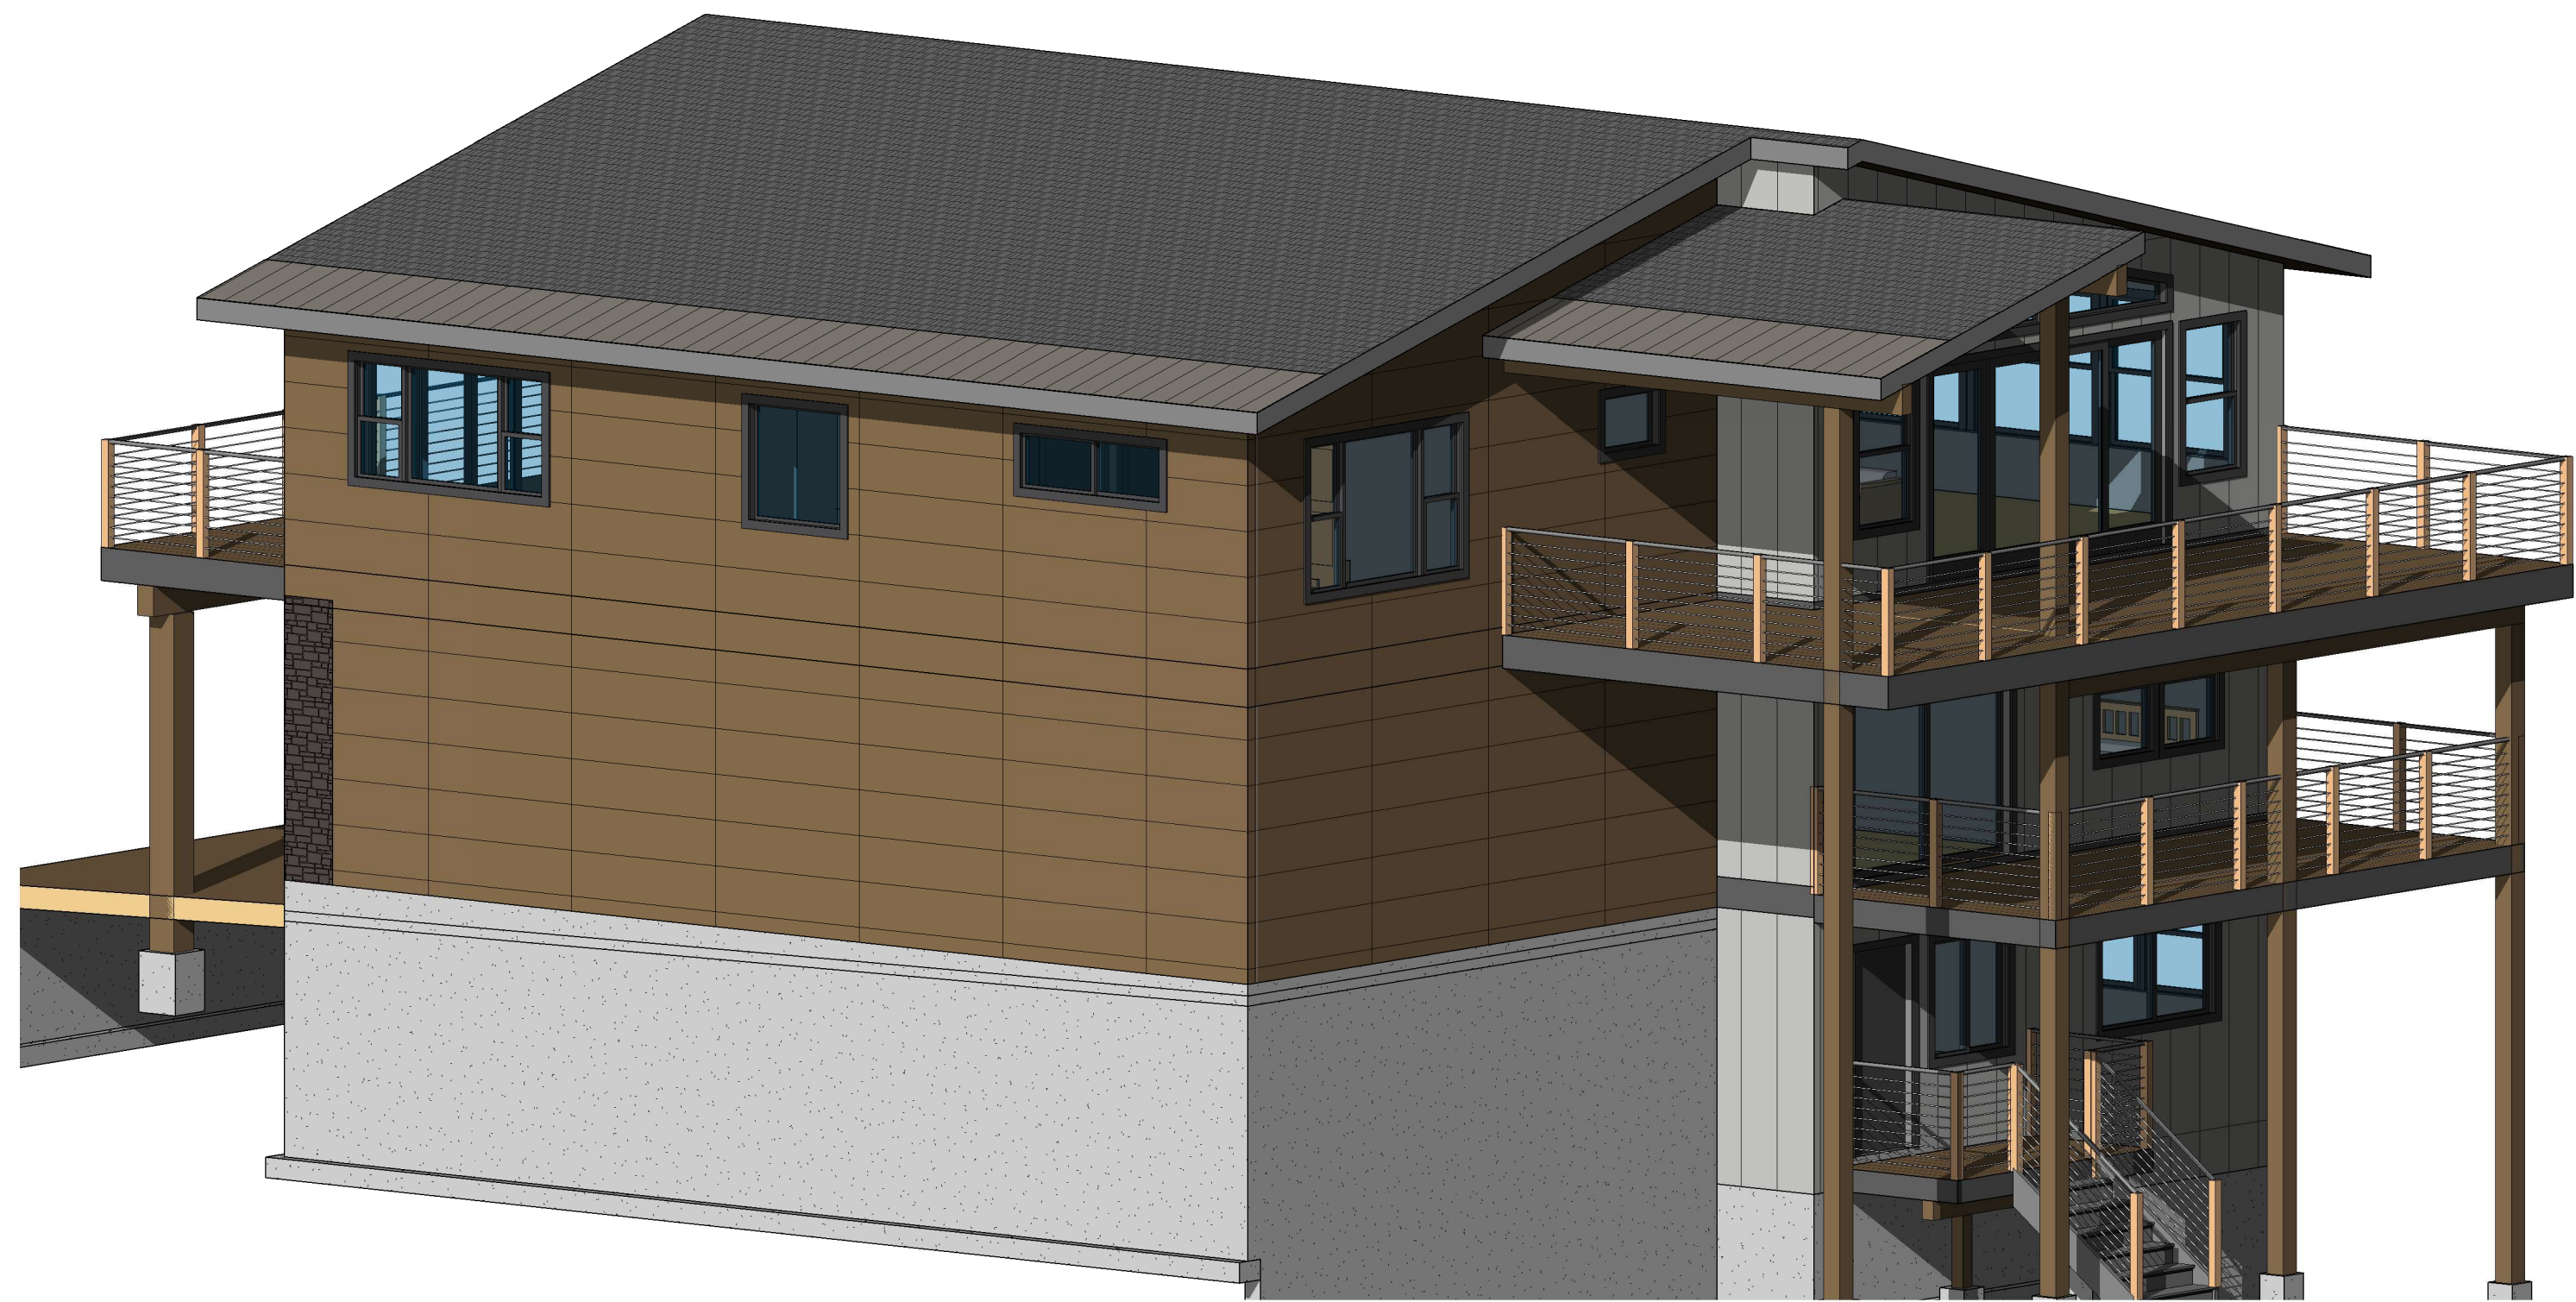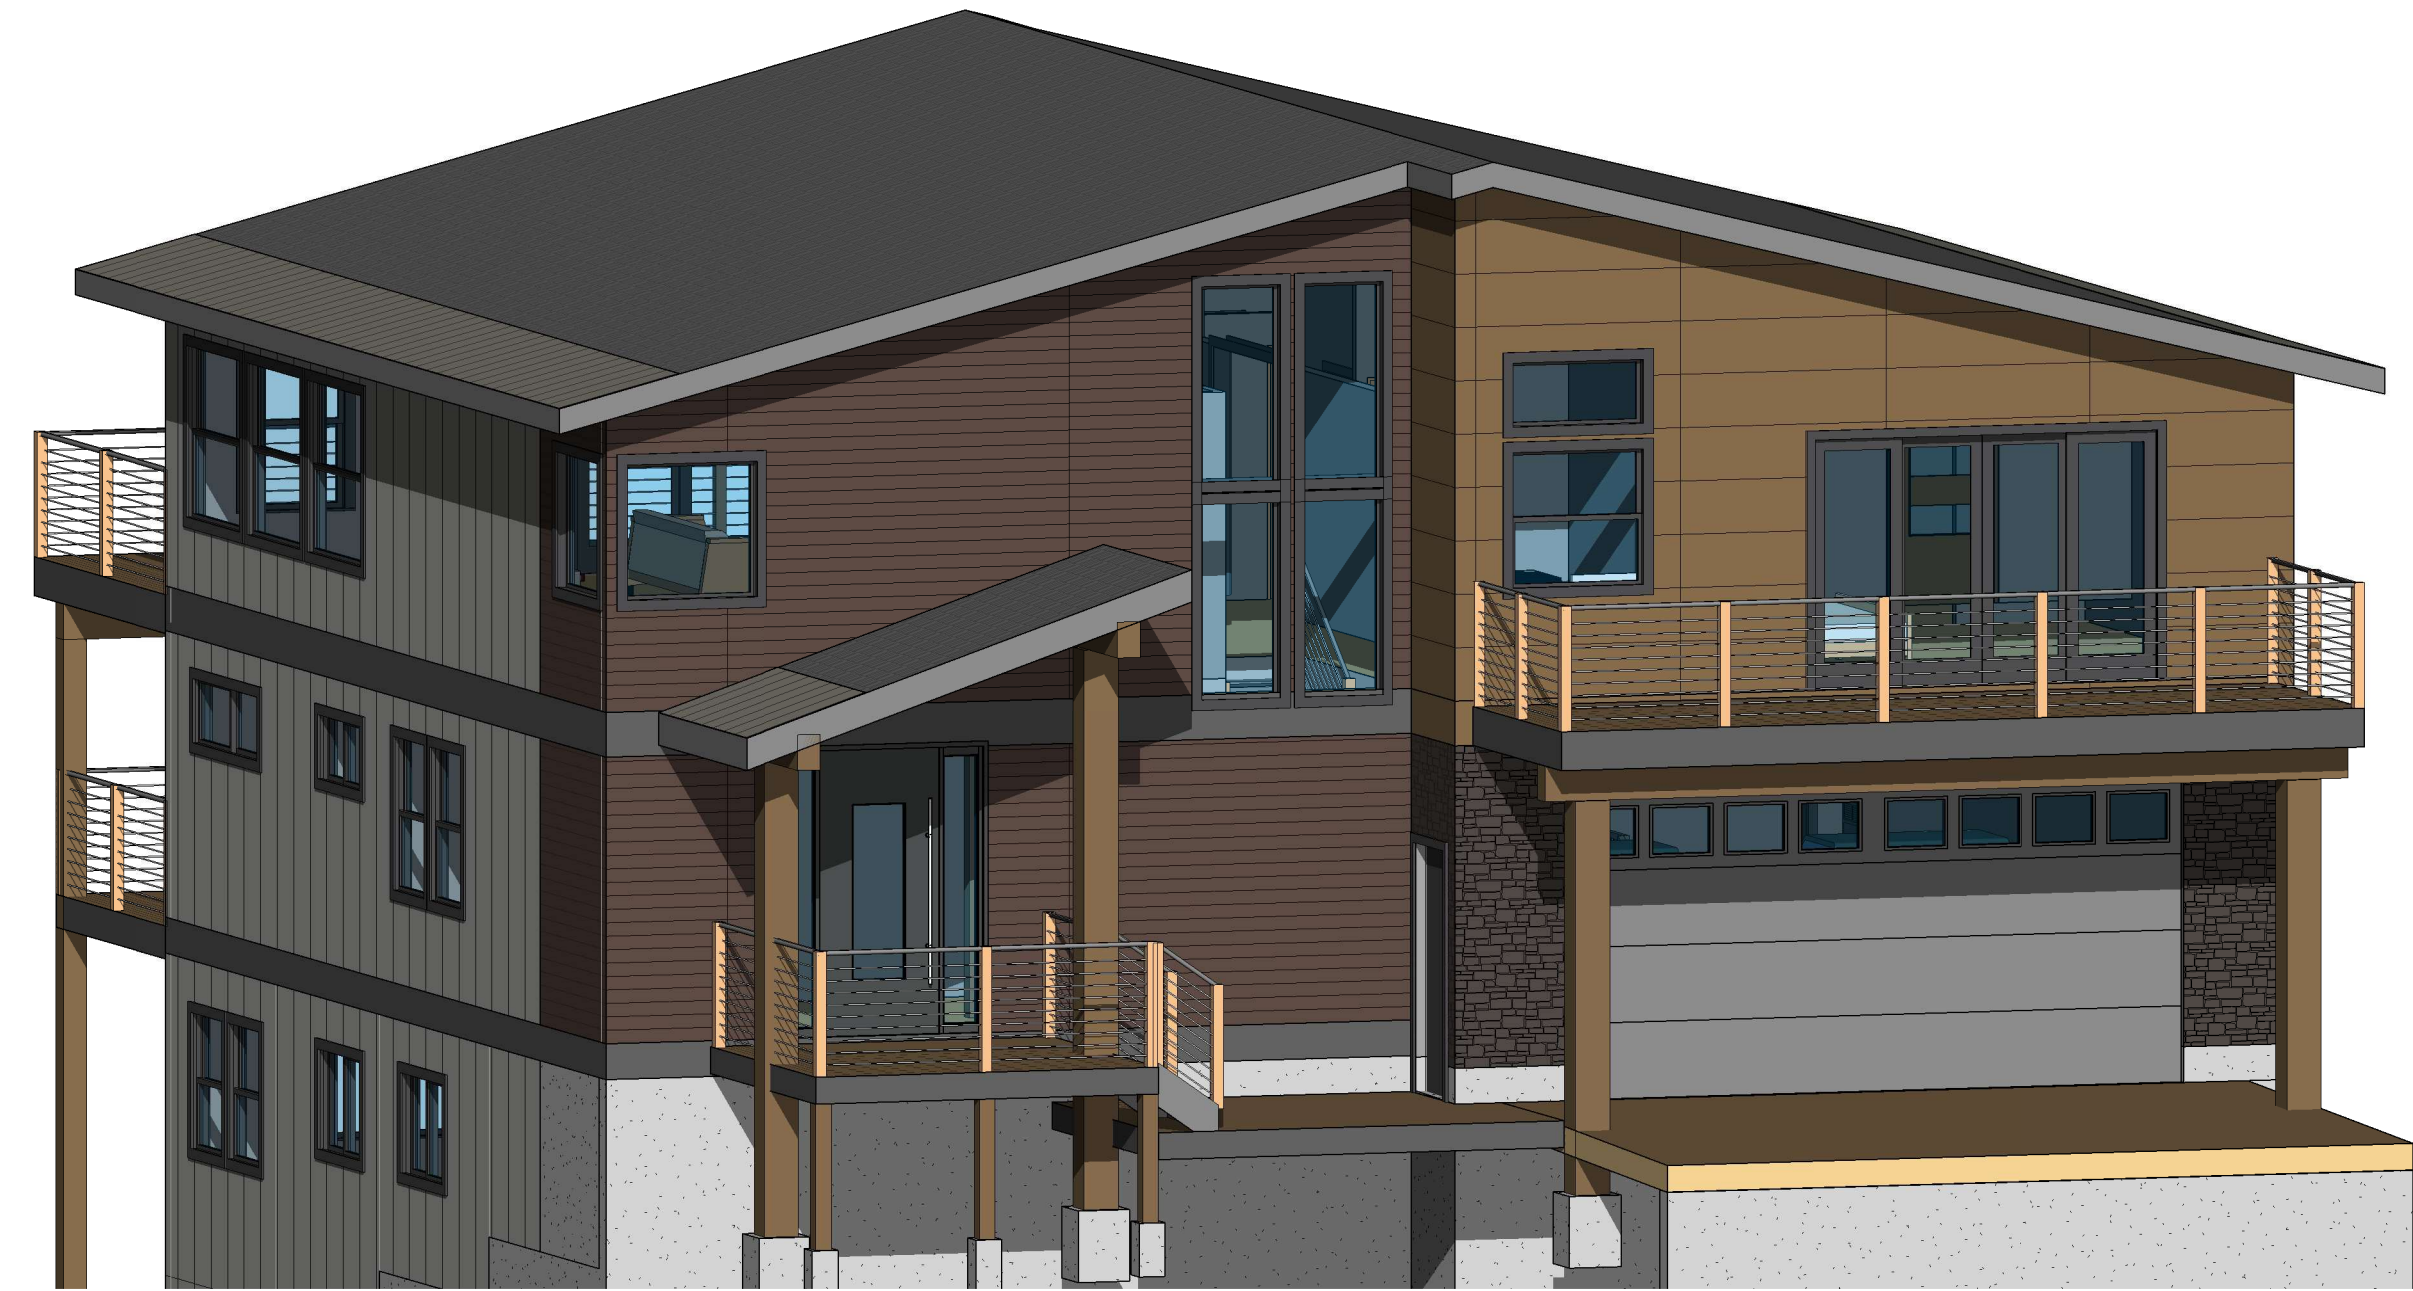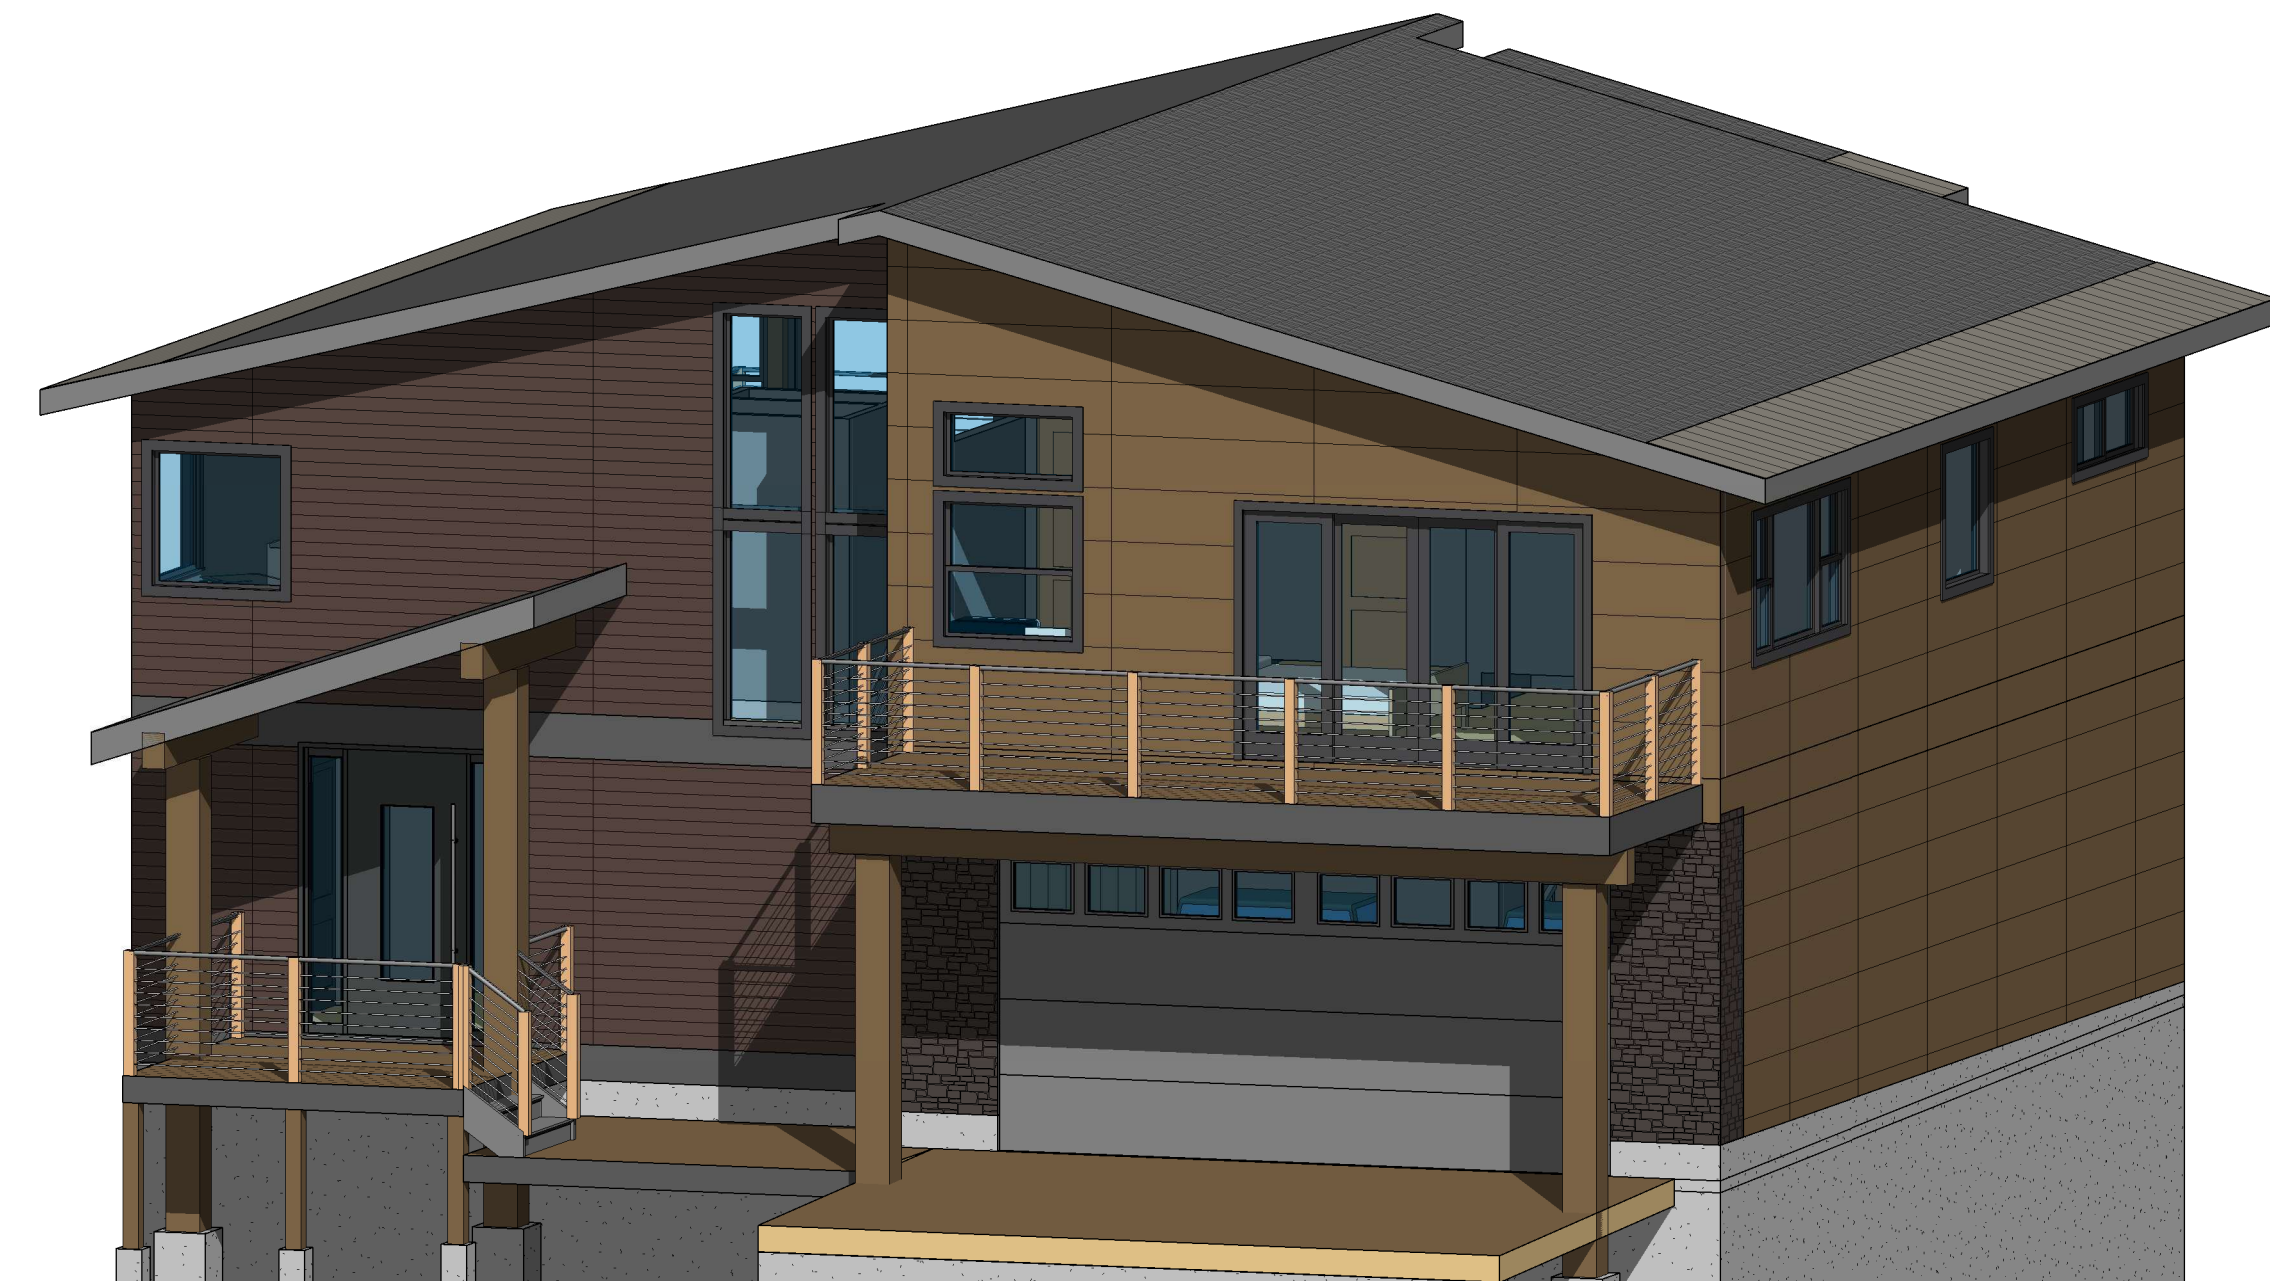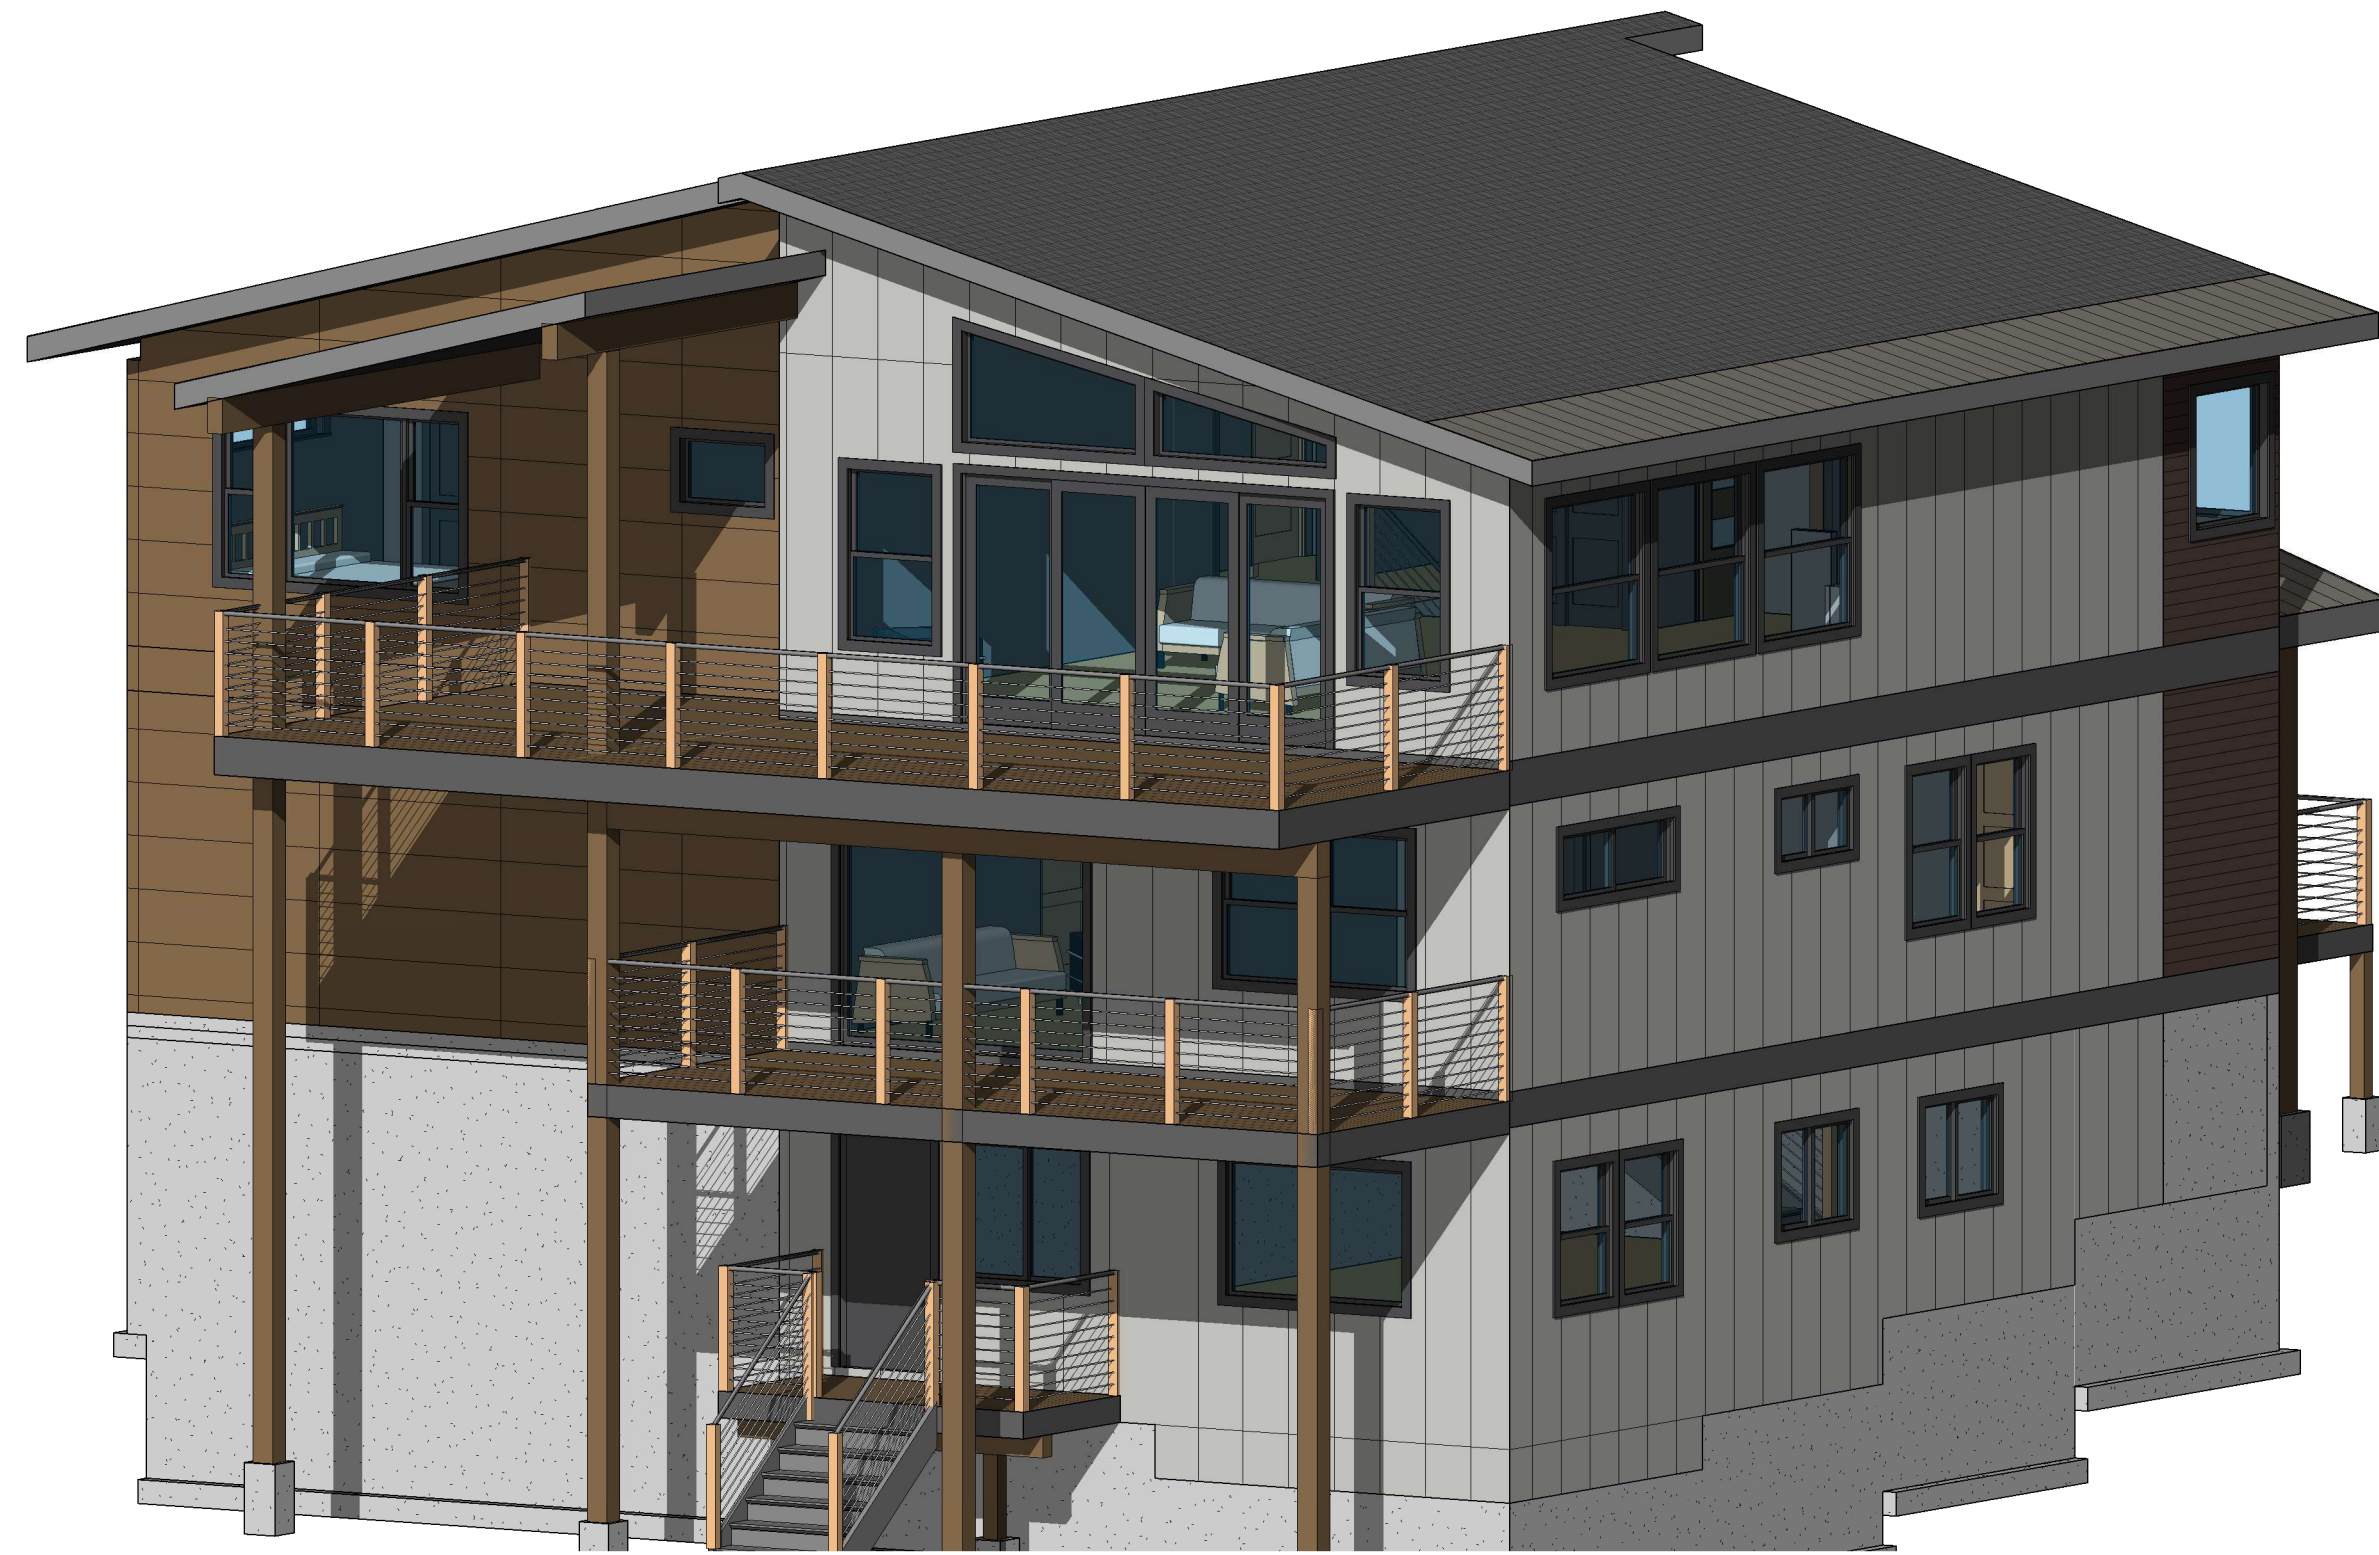

PROPOSED ISOMETRIC VIEWS


PROJECT FOR:
GRIFFIN RESIDENCE
795 COLUMBINE CIRCLE LOT 518
KIRKWOOD, ALPINE CO. CA 95646
APN: 006-152-001

REVISION:



ALL RIGHTS RESERVED
ALL DRAWINGS AND WRITTEN MATERIAL
APPEARING HEREIN CONSTITUTE THE ORIGINAL
WORK OF JA DESIGNS, INC.
AND THE SAME MAY NOT BE REPRODUCED,
USED, OR DISCLOSED WITHOUT THE WRITTEN
CONSENT OF JA DESIGNS

JOB No:
DRAWN BY: SB
CHECKED BY:
DATE PREPARED: 2026
SCALE: as noted
FILE:

DRAWING No:

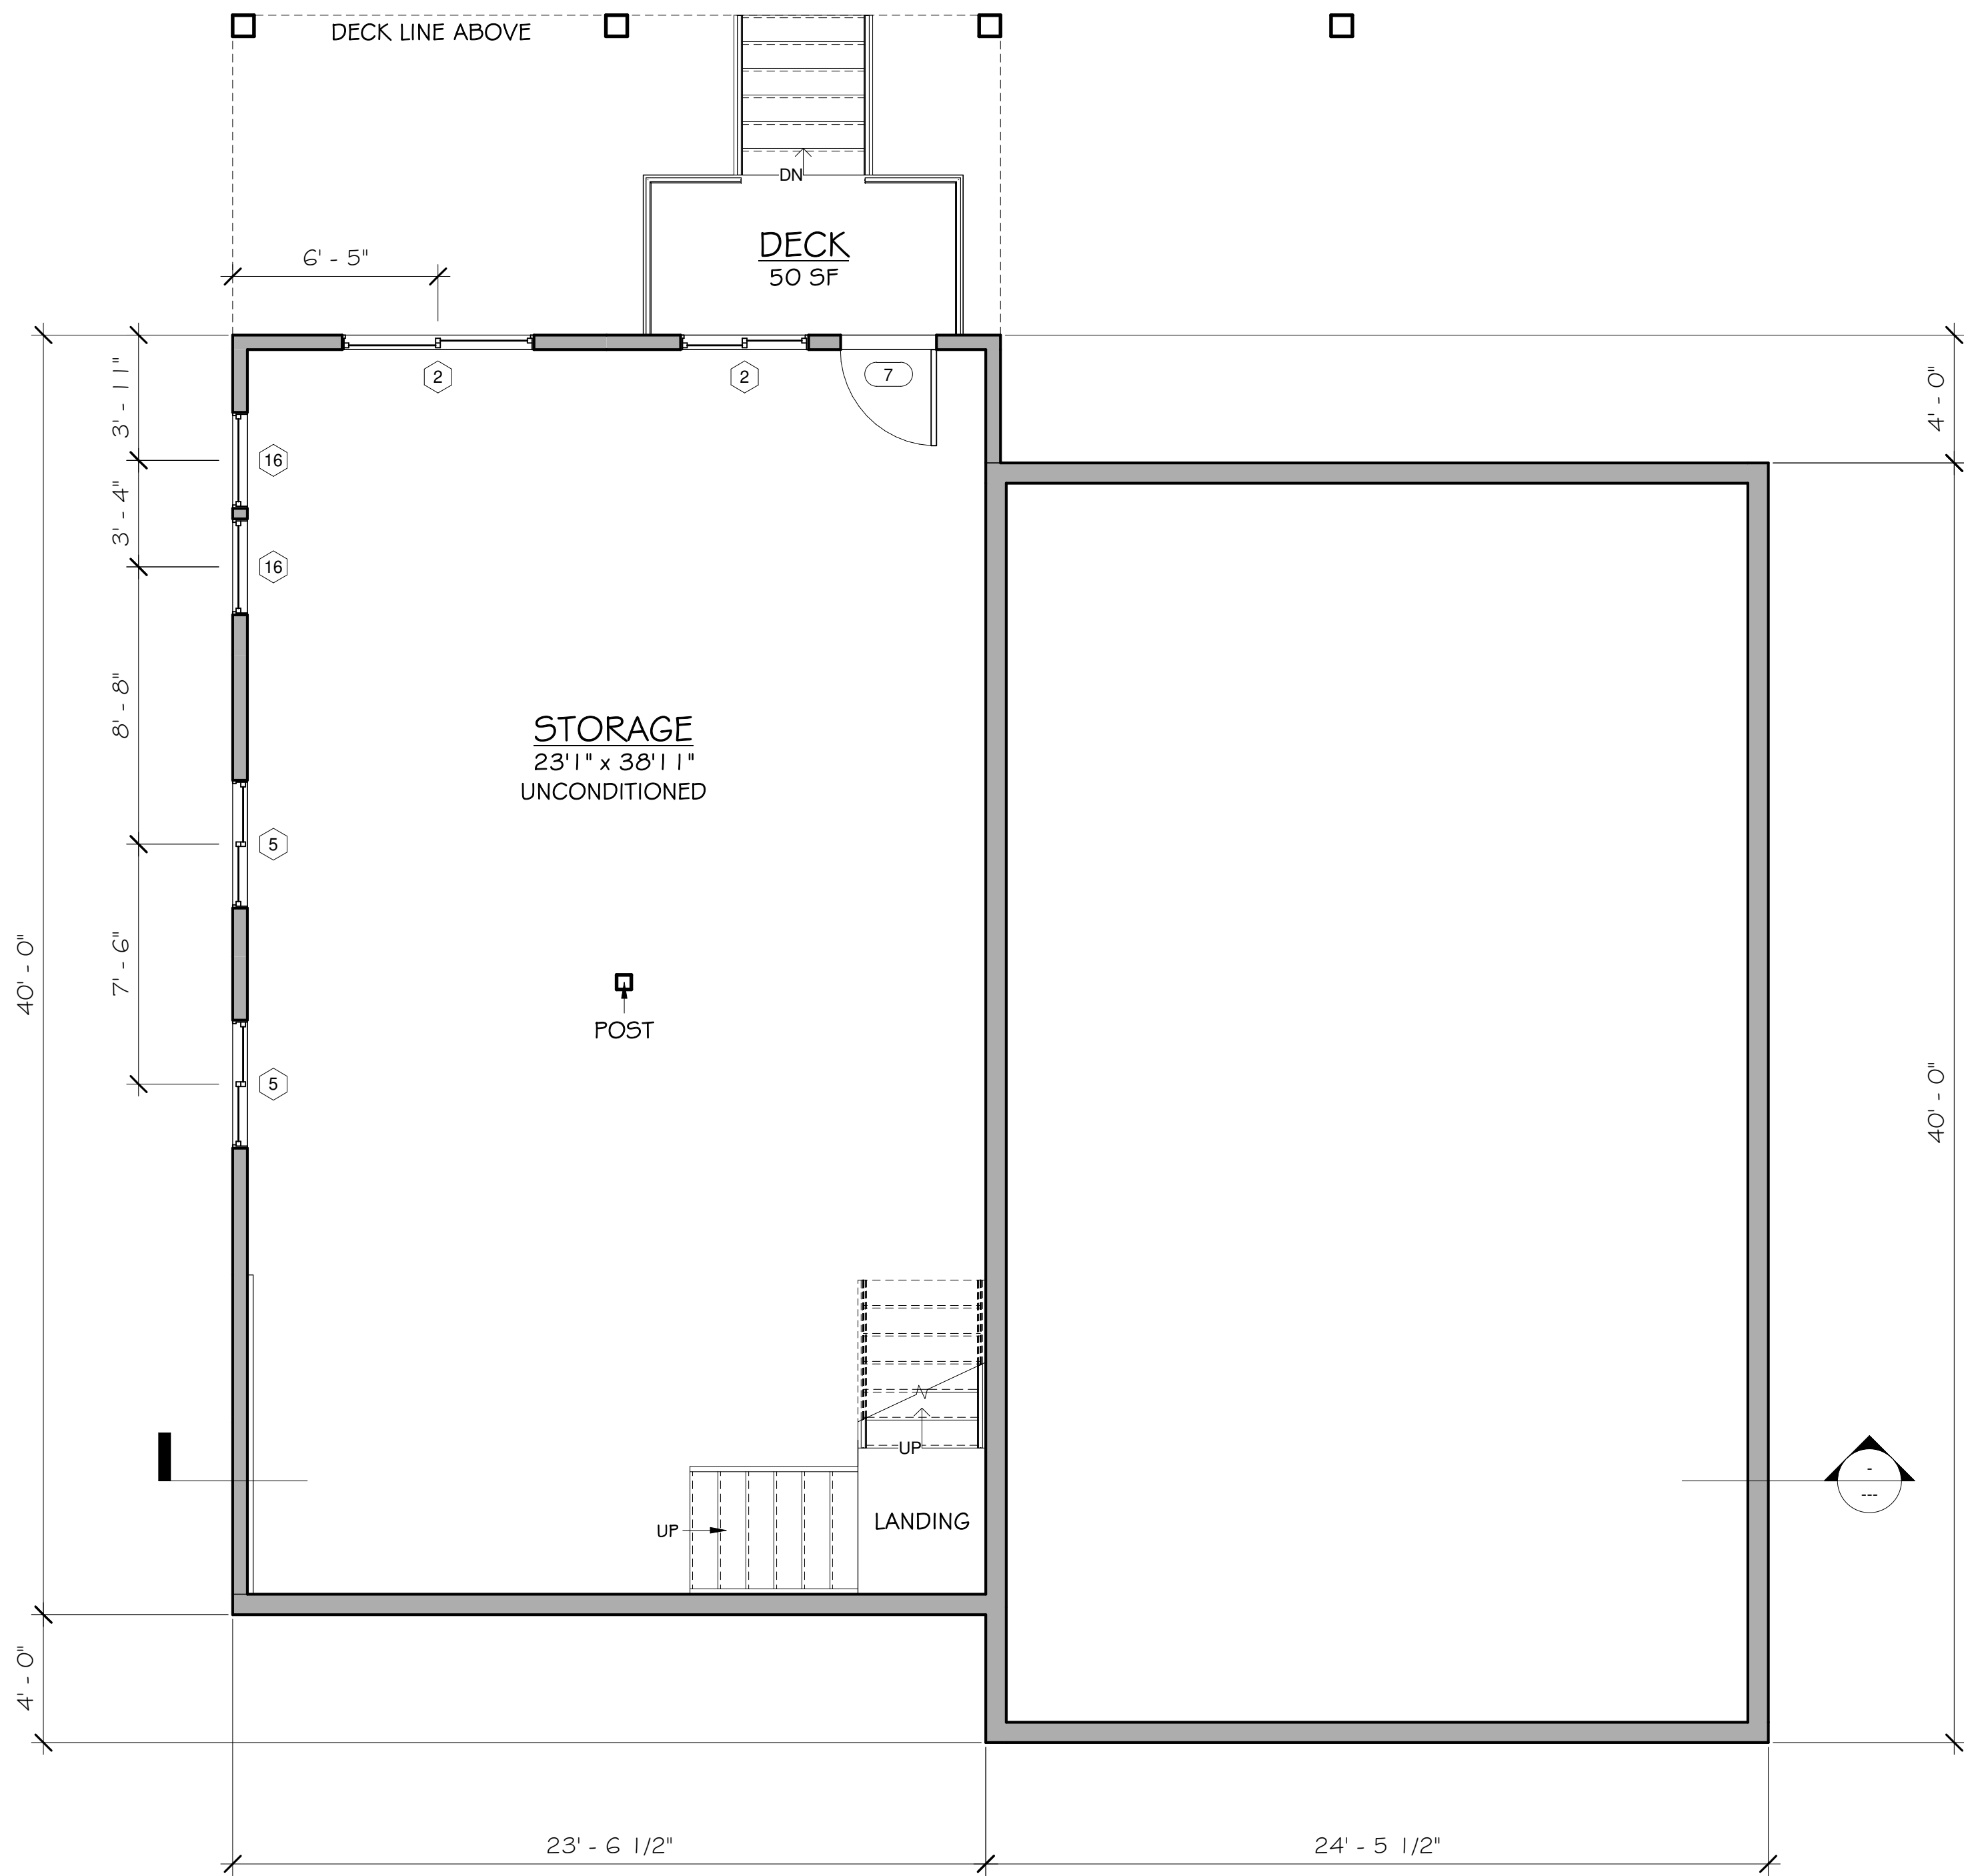

PROPOSED BASEMENT FLOOR PLAN
SCALE: 1/4" = 1' - 0"

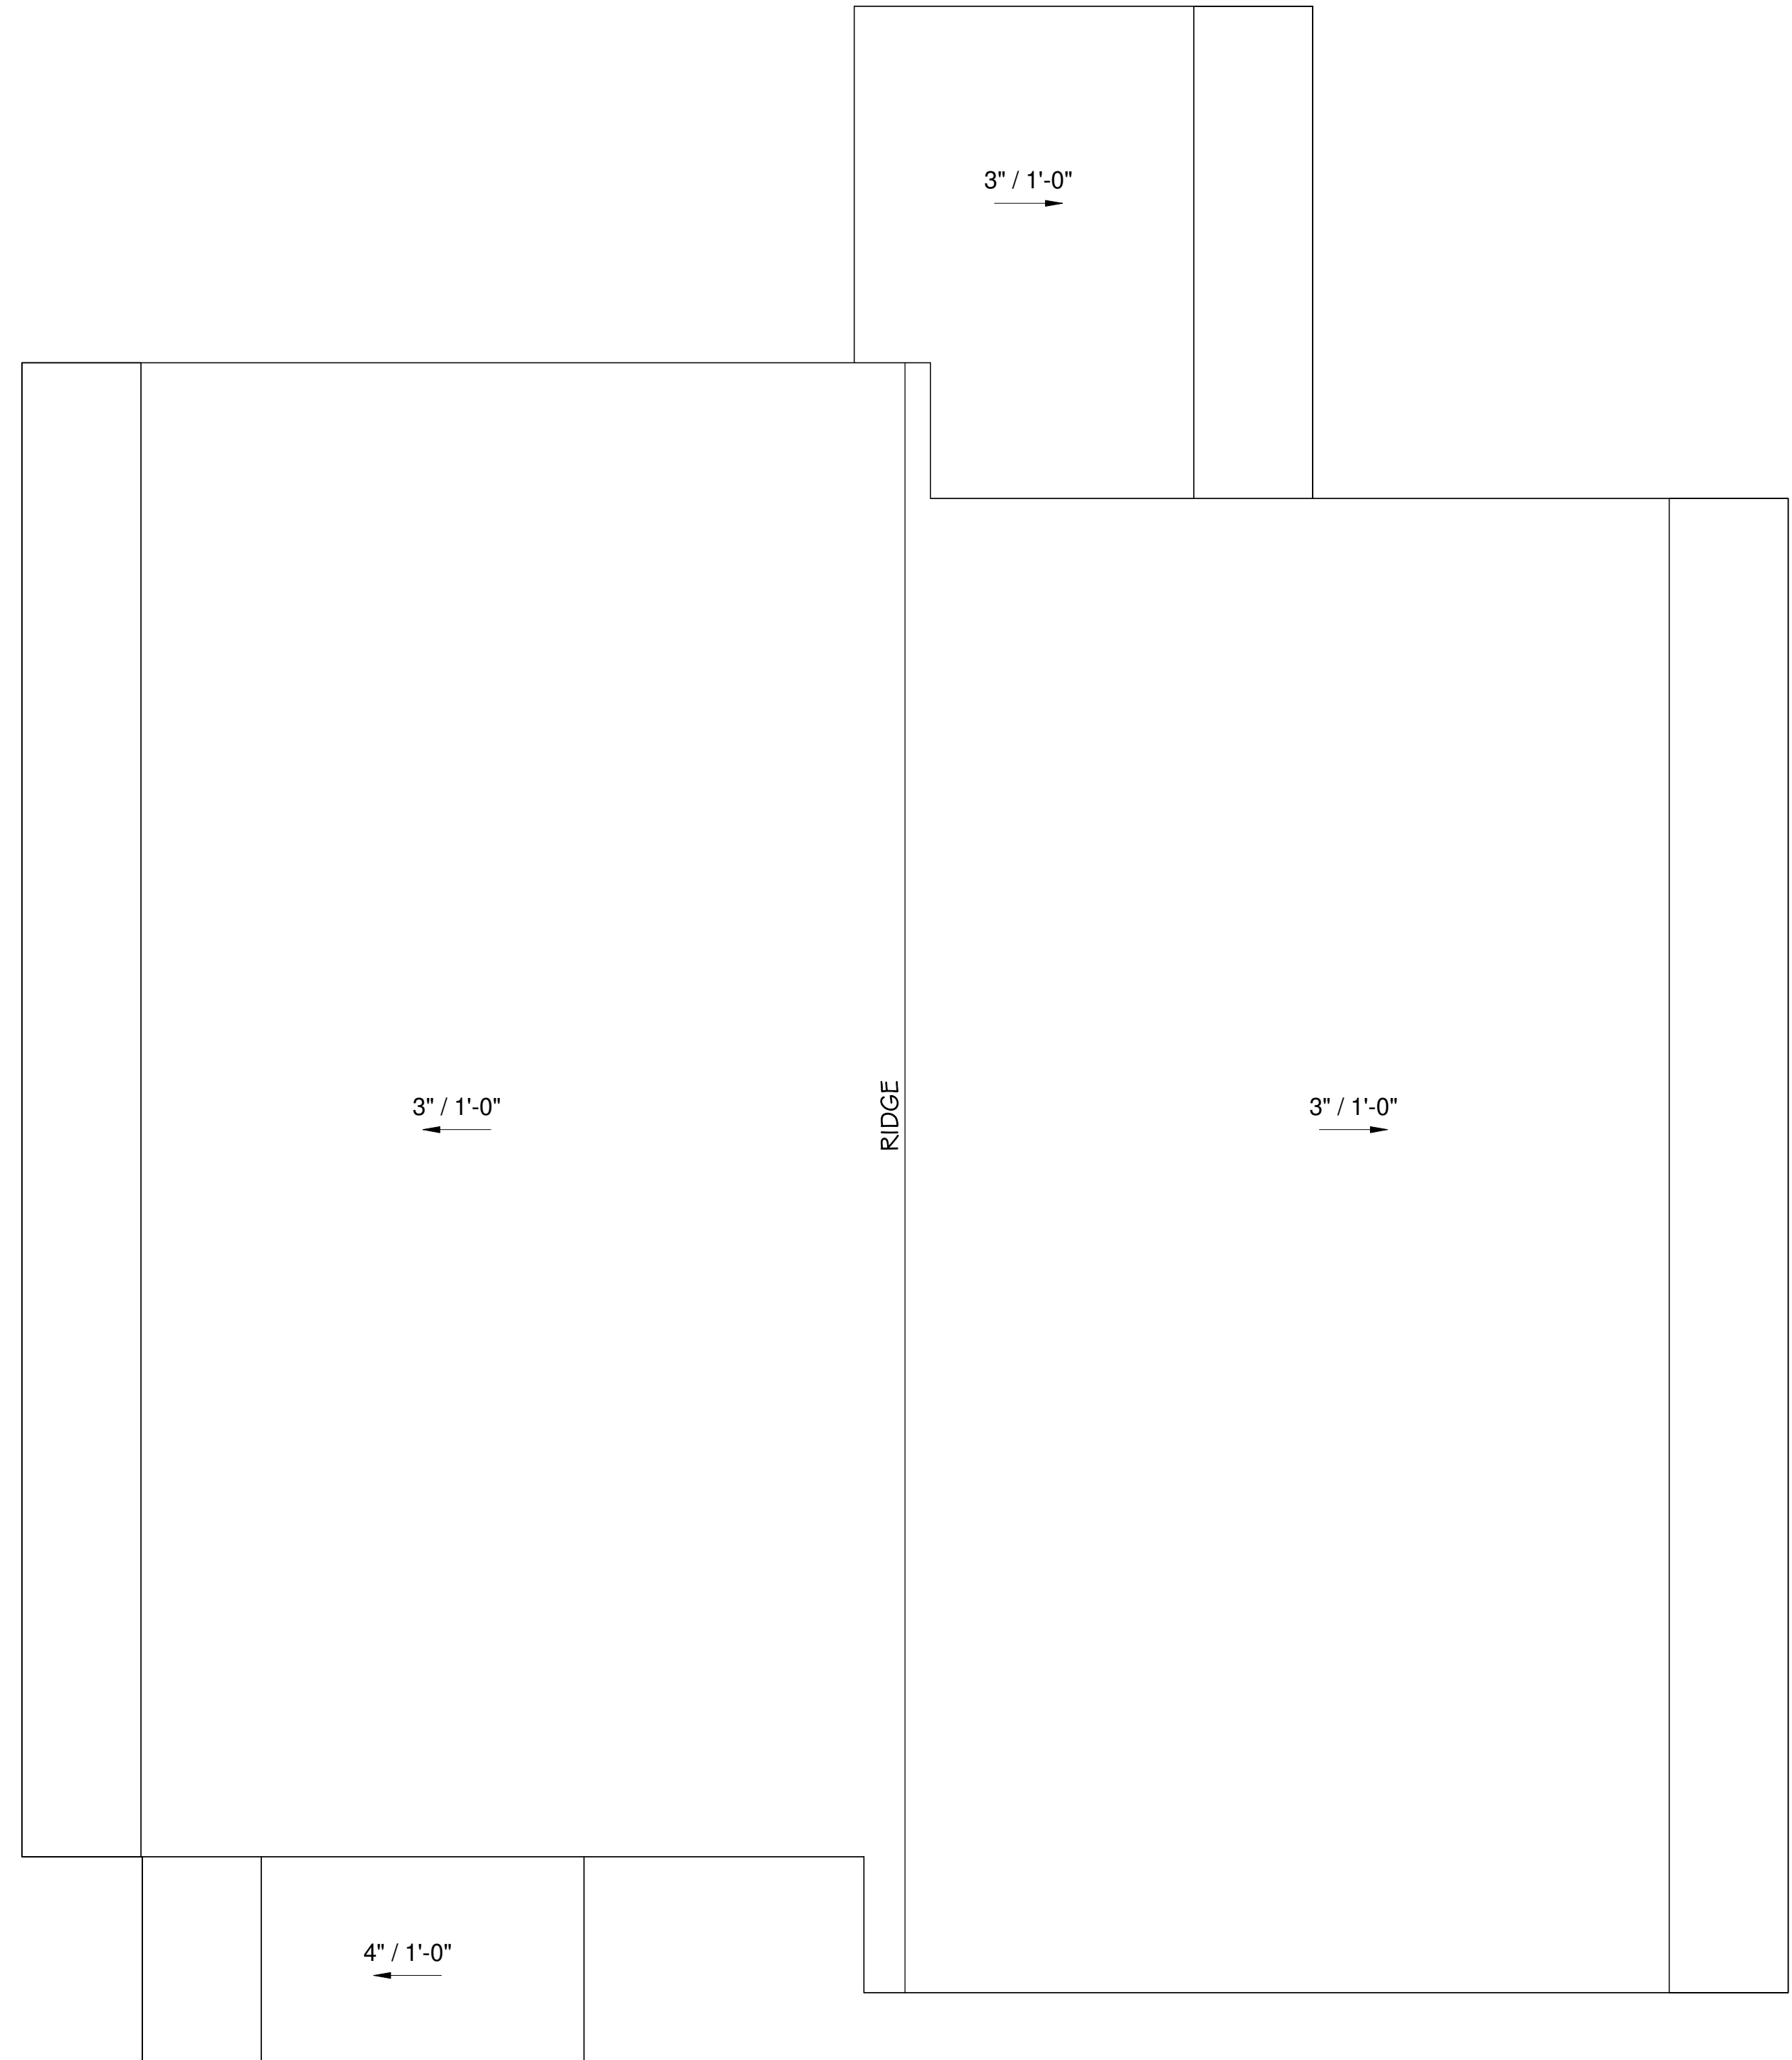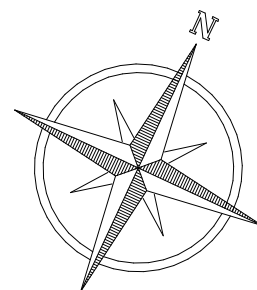

PROPOSED ROOF PLAN
SCALE: 1/4" = 1' - 0"

**PROPOSED STORAGE FLOOR PLAN
& ROOF PLAN**

PROJECT FOR:
GRIFFIN RESIDENCE
795 COLUMBINE CIRCLE LOT 518
KIRKWOOD, ALPINE CO. CA 95646
APN: 006-152-001

REVISION:

JA DESIGNS
ALL RIGHTS RESERVED
ALL DRAWINGS AND WRITTEN MATERIAL
APPEARING HEREIN CONSTITUTE THE ORIGINAL
UNPUBLISHED WORK OF
JA DESIGNS
AND THE SHOWN HEREIN BE REPRODUCED,
USED, OR DISCLOSED WITH-OUT THE WRITTEN
CONSENT OF JA DESIGNS

JOB No:
DRAWN BY: SB
CHECKED BY:
DATE PREPARED: 2026
SCALE: as noted
FILE:

DRAWING No:

A5